


Наименование	ТН-1 10 Т-21 (60BAA21 GT121)	ТН-2 10 Т-21 (60BAA21 GT221)	Положение в АСУ ТП	Цепи ТТ ТСН	Цепи освещения
Обозначение					
Номер монтажной единицы	01	02	03	04	00

Примечания:


1. По данному чертежу изготовить один навесной шкаф размерами 1200х600х400.
2. Климатическое исполнение шкафа УХЛ4.
3. Конструкция шкафа должна обеспечивать защиту размещенных в нем аппаратов со степенью не хуже IP54.
4. Сейсмостойкость шкафа по шкале MSK-64 - 9 баллов
5. Металлоконструкция шкафа должна иметь порошковое покрытие светло-серого цвета RAL7035.
6. Подвод контрольных кабелей к шкафу осуществляется снизу.
7. В днище шкафа предусмотреть ступенчатые кабельные вводы для подвода кабелей.
8. В конструкции шкафа в качестве планки для ЭМС зажимов предусмотреть скобу - гребенку, с возможностью крепления кабелей с помощью экранирующих ЭМС и кабельных зажимов. Экранирующие зажимы ЭМС и кабельные зажимы должны входить в комплектацию шкафа.
9. Цепи освещения уточняются заводом-изготовителем. Евророзетка двойная, закрытая с заземлением.
10. Шкаф должен иметь информационную табличку на двери во всю ширину шкафа. Табличка выполняется из самоклеющейся бумаги с защитной пленкой или из тонкого пластика. Надпись выполняется шрифтом Arial с высотой букв 35 мм. Перед началом производства таблички произвести согласование макетов и материала с Заказчиком.
- 11.Под каждым аппаратом с лицевой стороны шкафа, а также под аппаратами, расположенными внутри шкафа, должны быть предусмотрены карманы маркировочные для соответствующего текста надписи
13. Для заземления резервных жил вторичных цепей, должны быть предусмотрены шинки вдоль боковин, соединенные с корпусом шкафа, либо клеммный ряд для заземления.
14. В нижней части шкафа предусмотреть медную шину для заземления всех нетоковедущих частей шкафа.
15. Выполнить подключение металлических частей шкафа заземляющим желто-зеленым проводником к шине заземления шкафа.
16. Указать место присоединения внешнего заземляющего устройства к корпусу шкафа.
17. Наклеить знаки "Заземление" около болтов и шины заземления, знак "Осторожно электрическое напряжение" наклеить на передней и задней дверях шкафа.
18. Монтаж внутри шкафа должен быть выполнен проводом с медной жилой и ПВХ изоляцией белого цвета с низким газо-и дымовыделением, не поддерживающим горение.
19. Монтаж в шкафу выполнить проводом сечением не менее 1,5 кв.мм для цепей тока, цепей напряжения, в цепях освещения и питания розеток шкафа и сечением 1 кв.мм для остальных цепей.
20. В шкафу предусмотреть короба для укладки проводов и для укладки жил кабелей рядом с клеммными зажимами, в объеме достаточном для укладки всех жил кабелей.
21. Двери шкафа должны закрываться стандартным замком (с двойной бороздкой).
22. Тип, количество зажимов и принадлежностей к клеммным зажимам определяет завод изготовитель из номенклатуры производителя клеммных зажимов.
23. Шкаф должен соответствовать требованиям, изложенные в Типовых проектных решениях ПАО "Русгидро" № 87-07-2015-РЗА.ТПР1.1 2024г
24. Укомплектовать ЗИП на гарантийный период

Инв. N подл.	Взам. инв. N	Подпись и дата	2261-26-102									
			Реконструкция ОП "Южно-Сахалинская ТЭЦ-1" путем строительства 6-го энергоблока мощностью 50 МВт с установкой двух газотурбинных энергоагрегатов ЭГЭС-25ПА									
			Изм.	Кол.уч.	Лист	N док.	Подпись	Дата				
			Разработал		Смирнова				Задание заводу-изготовителю на шкаф зажимов ТН и ТТ	Стадия	Лист	Листов
			Проверил		Обысова					Р	1	6
			Н.контроль		Габышева				Шкаф зажимов ТН и ТТ (60BAA21 GH01)			
			Нач.отд		Грибанов							


Вид спереди с дверью

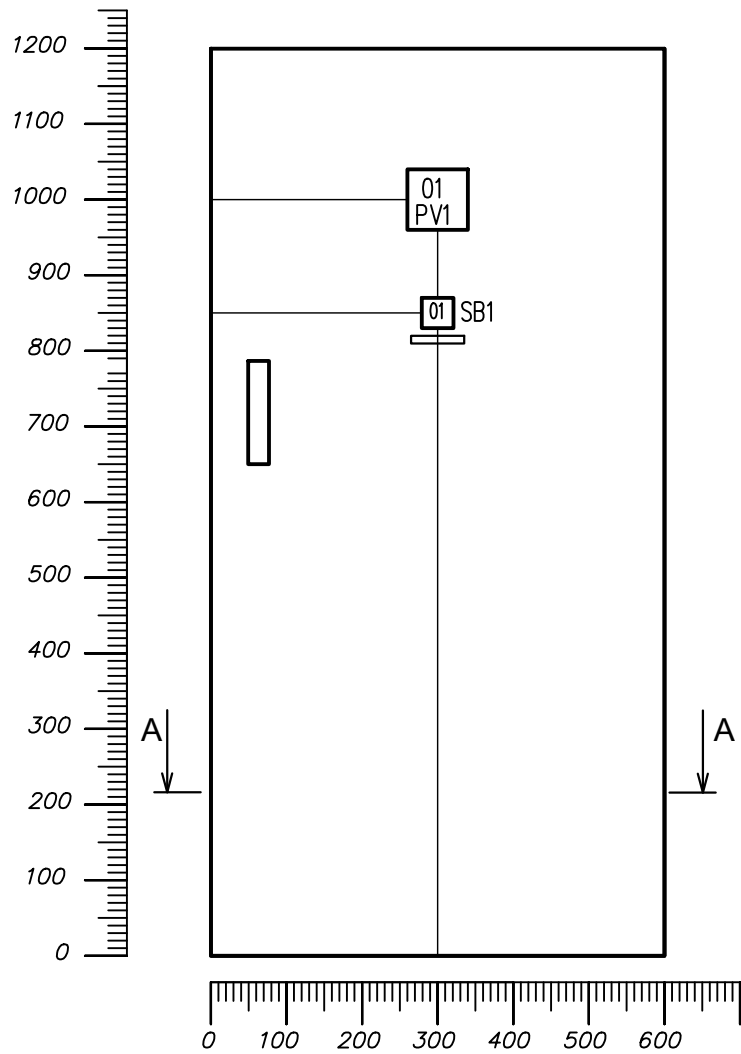

Вид спереди со снятой дверью

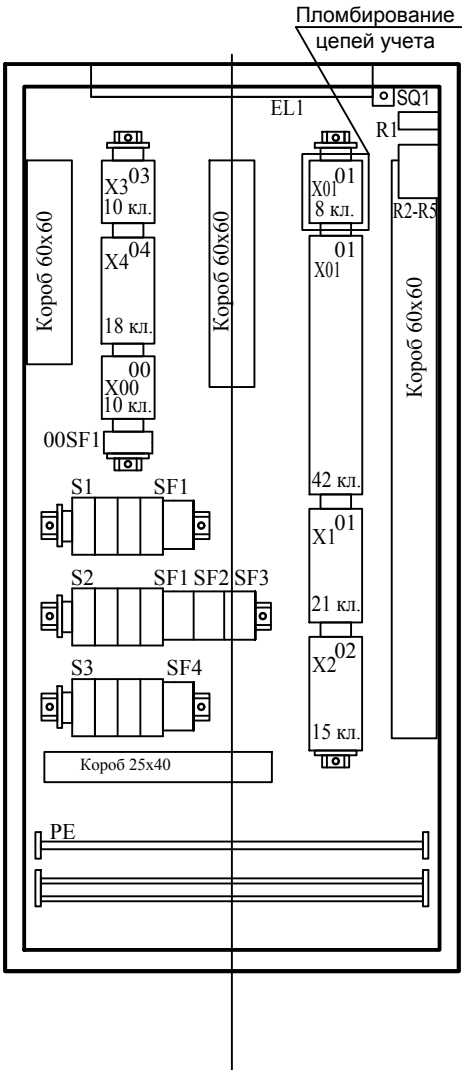


Вид сбоку

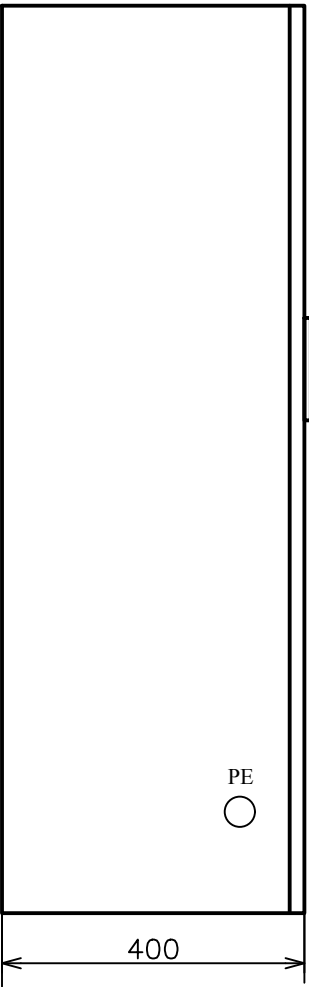

A-A

Дно шкафа. Подводка кабелей через сальники PG16, PG21

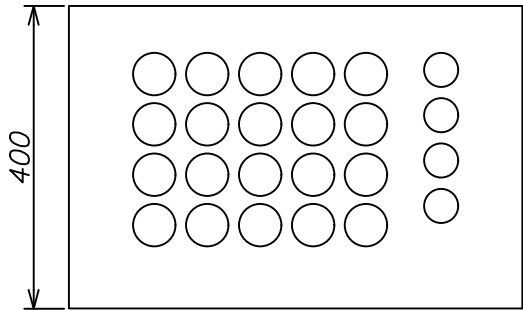


Информационная табличка

Шкаф зажимов ТН и ТТ	60BAA21 GH01
----------------------	--------------


2 шт.

Общий вид

						2261-26-102	Лист
Изм.	Кол.уч.	Лист	№ док.	Подпись	Дата		2

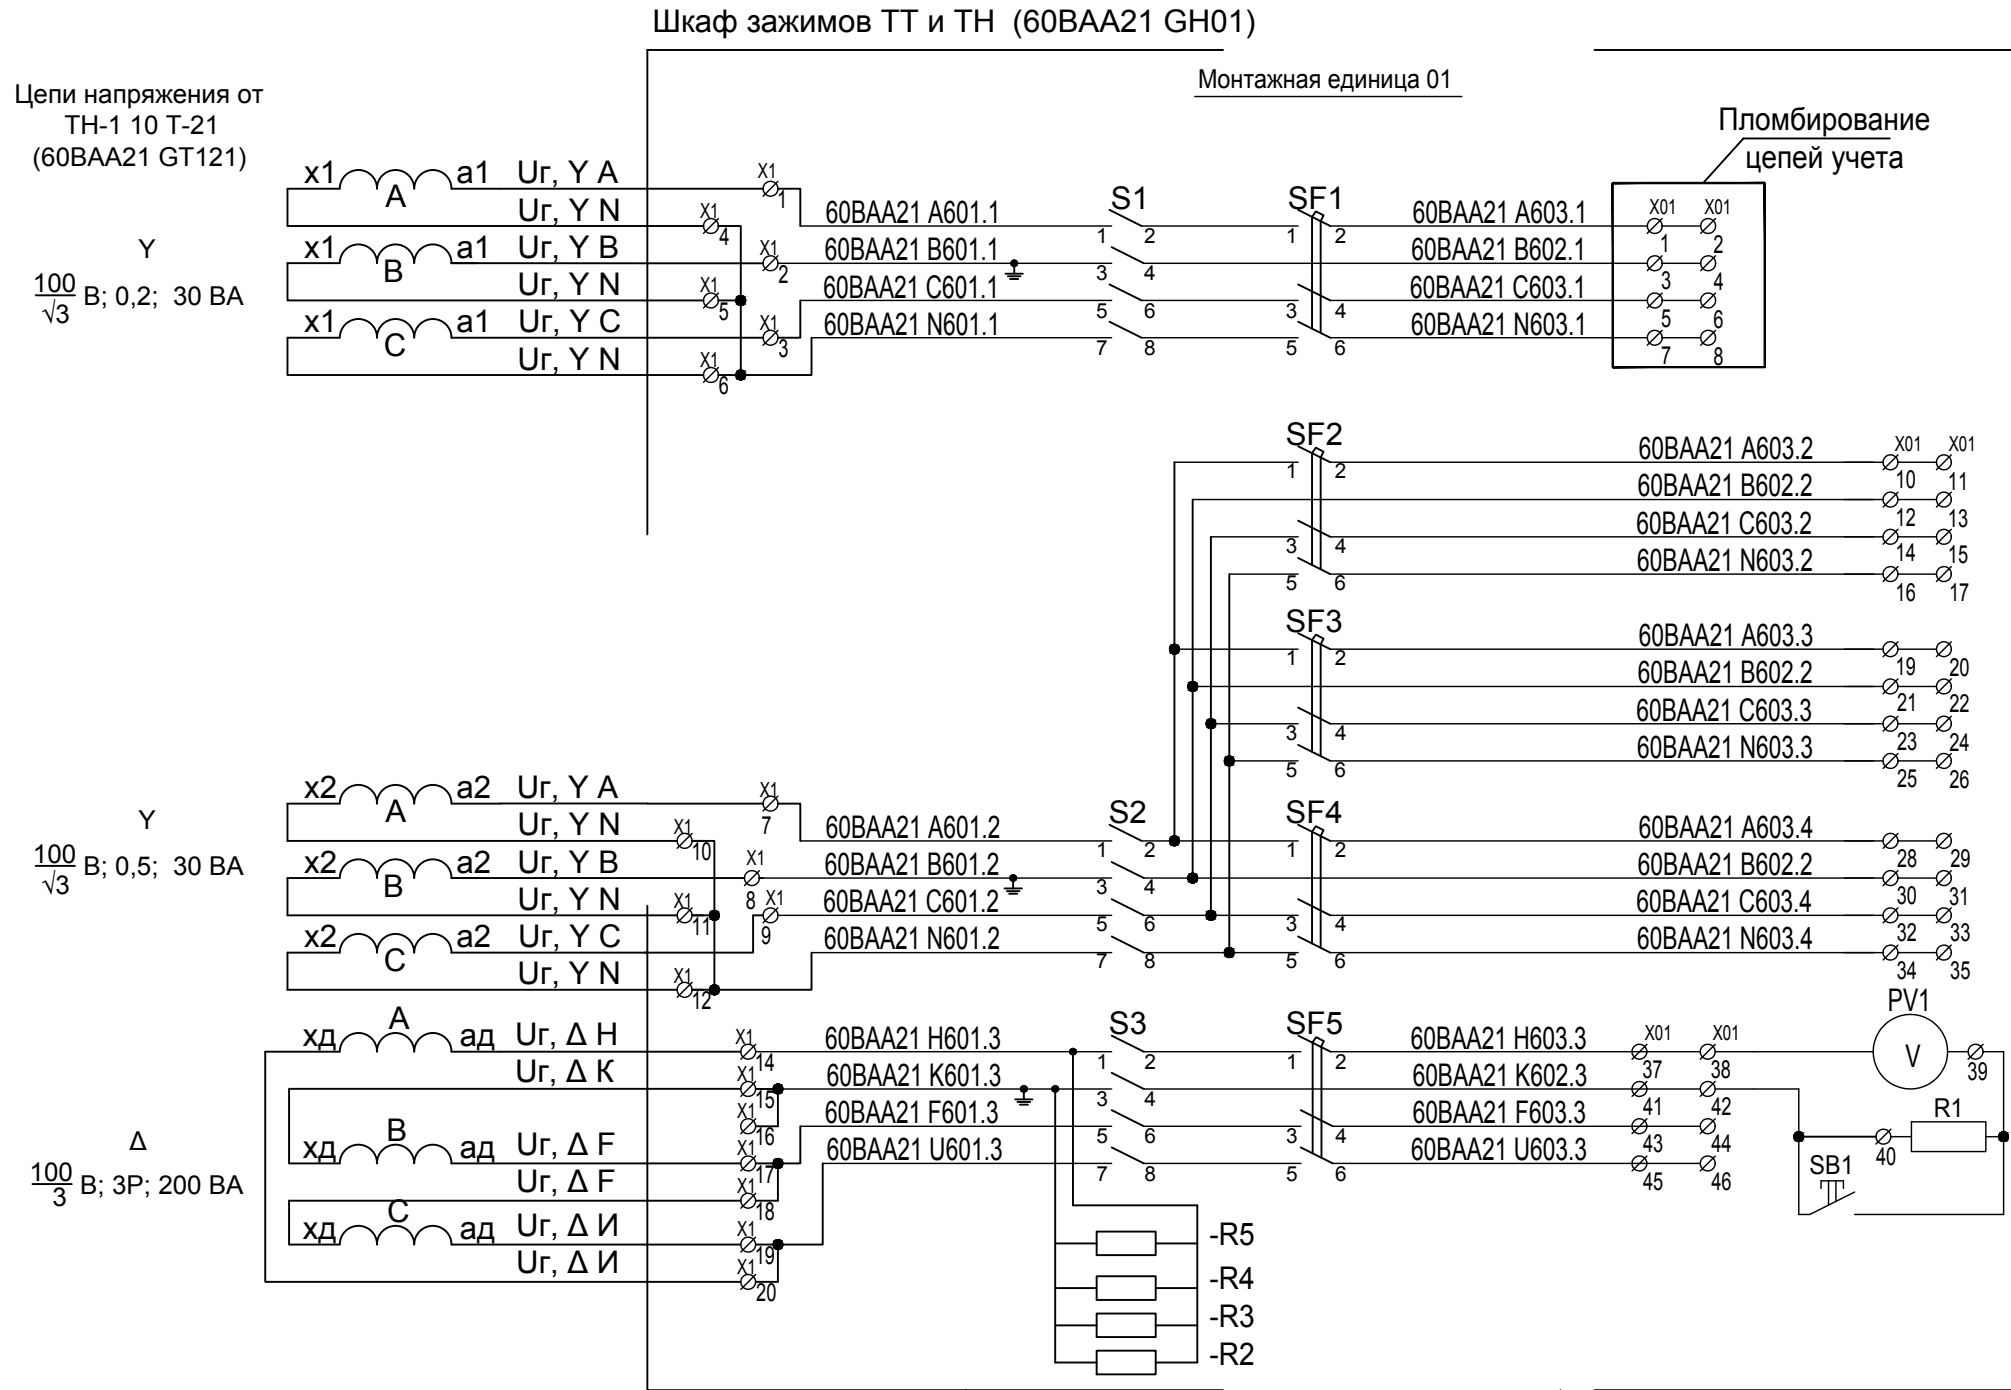

Изм.	Кол.уч.	Лист	№ док.	Подпись	Дата	2261-26-102	Лист 3
------	---------	------	--------	---------	------	-------------	--------

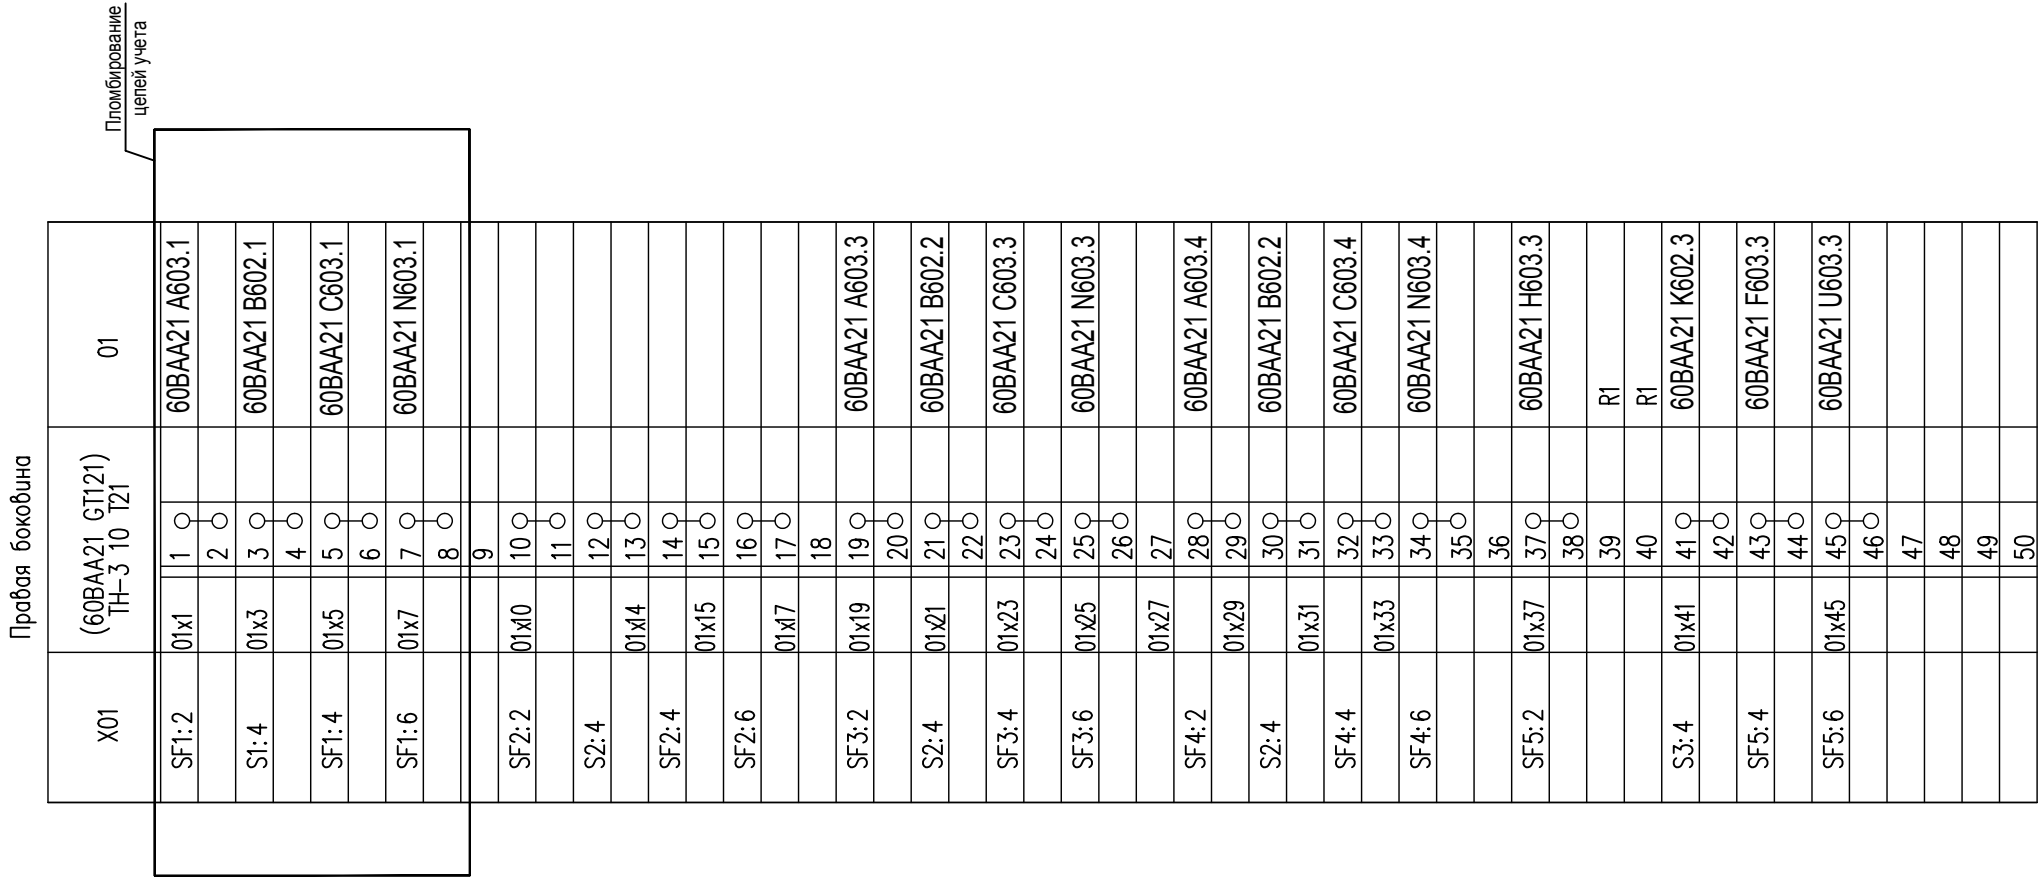

X3	Положение в АСУ ТП	03
	1 03x1	SF1:11
	2 03x1	SF4:11
	3 03x3	SF5:11
	4	
	5 03x5	SF1:12
	6 03x6	SF4:12
	7 03x7	SF5:12
	8	
	9	
	10	

X4	Цепи ТТ ТСН	04
	1 X4:1	A811-4
	2 X4:2	B811-4
	3 X4:3	C811-4
	4 X4:4	
	5 ○ X4:5	N811-4
	6 ○ X4:6	
	7 ○ X4:7	
	8 ○ X4:8	
	9 X4:9	
	10 X4:10	A811-3
	11 X4:11	B811-3
	12 X4:12	C811-3
	13 X4:13	
	14 ○ X4:14	N811-3
	15 ○	
	16 ○	
	17 ○	
	18	

X00	Цепи освещения	00
SF1:1	1 ○	L1
	2 ○	L1
	3	
SF1:3	4 ○	N
	5 ○	N
	6	
	7 ○	PE
	8 ○	PE

X2	(60BAA21 GT221) TH-4 10 T21	02
	1	X5:1 A601
	2	X5:2 B601
	3	X5:3 C601
	4	X5:4 ○ N601
	5	X5:5 ○
	6	X5:6 ○
	7	
	8	X5:8 H601
	9	X5:9 ○ K601
	10	X5:10 ○
	11	X5:11 ○ F601
	12	X5:12 ○
	13	X5:13 ○ U601
	14	X5:14 ○
	15	

X1	(60BAA21 GT121) TH-3 10 T21	01
A601.1	1	X1:1 S1:1
B601.1	2	X1:2 S1:3
C601.1	3	X1:3 S1:5
N601.1	4 ○	X1:4 S1:7
N601.1	5 ○	X1:5
N601.1	6 ○	X1:6
A601.2	7	X1:7 S2:1
B601.2	8	X1:8 S2:3
C601.2	9	S2:5
N601.2	10 ○	X1:10 S2:7
	11 ○	X1:11
	12 ○	X1:12
	13	
H601.3	14	X1:14 S3:1
K601.3	15 ○	X1:15 S3:3
	16 ○	X1:16
F601.3	17 ○	X1:17 S3:5
	18 ○	X1:18
U601.3	19 ○	X1:19 S3:7
	20 ○	X1:20
	21	

Схема электрическая соединений рядов зажимов

Перечень надписей

Поз.	Место надписи	Текст надписи	Примечание
SB1	в рамке	Напряжение небаланса ТН-3 10 Т21 10,5кВ /Замер небаланса 3Uo	
PV1	в рамке	Напряжение небаланса ТН-3 10 Т21 10,5кВ /Замер небаланса 3Uo	
S1	в рамке	цепи переменного напряжения "звезды" ТН-3 10 Т21 АИISKУЭ	
S2	в рамке	цепи переменного напряжения "звезды" ТН-3 10 Т21	
S3	в рамке	цепи переменного напряжения "треугольника" ТН-3 10 Т21	

Инв. N подл.	Подпись и дата	Взам. инв. N

Изм.	Кол.уч.	Лист	№ док.	Подпись	Дата

2261-26-102

Поз. обозн. и N монтаж. единицы	Обозначение	Наименование	Кол.	
		Шкаф зажимов ТН и ТТ нетиповой	1	Габариты 1200х600х400
01 PV1		Вольтметр		
		Э-365, шкала 0...150 В	1	
01 SB1		Кнопка КЕ - 011 исп. 4	1	
01 R1		Резистор ПЭВР-50 1500 Ом ± 10 %	1	
01 S1, S2,		Рубильник 250В, In=16А		
S3		P231111	3	
01 SF1,SF2,		Автоматический выключатель		
SF3,SF4,		Inом=4А Isраб=5-10Inом		
SF5		C60N C N 24347	5	
01 R2-R5		Резистор 100 Вт, 100 Ом C5-35В	4	
00 SQ2		Концевой выключатель двери		
		ВВП11-10Б 313 20У314	1	
00 XS1,XS2		Розетка с заземляющим контактом,		
		16А, 250В, 50Гц Арт.: mdse-47-pro РДЕ	2	
00 EL1		Светильник светодиодный щитовой		
		220В, 5Вт, магнит		
		ELM025 арт. ELM025	1	
00 SF1		Выключатель автоматический 2Р, 2А, С		
		ВМ63-2С2-УХЛ3 арт. 260603	1	
X1, X2,		Измерительная клемма с ползунковым		
X01		размыкателем РТМЕ 4	86	
X4		Измерительная клемма с ползунковым		
		размыкателем УТ 6-Т-НВ	18	
X3, X00		Измерительная клемма с ползунковым		
		размыкателем РТУ 6-Т-Р	18	
		Скоба - гребенка ЦИ.745322.001	2	
		Зажим ЭМС для экрана кабеля		см. лист 2
		Кабельный зажим		см. лист 2

Таблица УК и технические данные аппаратуры по заказу

						2261-26-102	Лист
							6
Изм.	Кол.уч.	Лист	№ док.	Подпись	Дата		

Взам. инв. N

Подпись и дата

Инв. N подл.