

Свидетельство о допуске к определенному виду работ, которые оказывают влияние на безопасность объекта капитального строительства № 0073.03-2017-7735116621-П-163 от 11.05.2017

**ПРОВЕДЕНИЕ РАБОТ ПО БЛАГОУСТРОЙСТВУ ТЕРРИТОРИИ
(ЕЕ ЭЛЕМЕНТОВ) ДЛЯ СОЗДАНИЯ «УМНОЙ» СПОРТИВНОЙ ПЛОЩАДКИ
ПО АДРЕСУ:
КАДАСТРОВЫЕ НОМЕРА УЧАСТКОВ: 63:01:0104002:1115,
63:01:0104002:1117.
САМАРСКАЯ ОБЛАСТЬ, Г. САМАРА, ЖЕЛЕЗНОДОРОЖНЫЙ РАЙОН, УЛ.
СПОРТИВНАЯ.**

РАБОЧАЯ ДОКУМЕНТАЦИЯ

Раздел ЭС «Внутриплощадочные сети электроснабжения. Устройство резервных кабельных линий»

З9МЗ-Р-2024-ЭС.1

Изм.	№ док.	Подп.	Дата

Свидетельство о допуске к определённому виду работ, которые оказывают влияние на безопасность объекта капитального строительства № 0073.03-2017-7735116621-П-163 от 11.05.2017

**ПРОВЕДЕНИЕ РАБОТ ПО БЛАГОУСТРОЙСТВУ ТЕРРИТОРИИ
(ЕЕ ЭЛЕМЕНТОВ) ДЛЯ СОЗДАНИЯ «УМНОЙ» СПОРТИВНОЙ ПЛОЩАДКИ
ПО АДРЕСУ:
КАДАСТРОВЫЕ НОМЕРА УЧАСТКОВ: 63:01:0104002:1115,
63:01:0104002:1117.
САМАРСКАЯ ОБЛАСТЬ, Г. САМАРА, ЖЕЛЕЗНОДОРОЖНЫЙ РАЙОН, УЛ.
СПОРТИВНАЯ.**

РАБОЧАЯ ДОКУМЕНТАЦИЯ

Раздел ЭС «Внутриплощадочные сети электроснабжения. Устройство резервных кабельных линий»

39МЗ-Р-2024-ЭС.1

Изм.	№ док.	Подп.	Дата


Взам.инв. №	
Подп. и дата	
Инв. № подл.	

Директор департамента



Анисимов И.В.

Главный инженер проекта

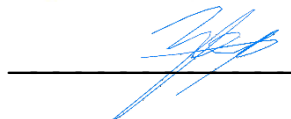

Зверобоев О.Л.

2025

Согласовано

Взам инв. №

Подл. и дата

Инв. № подл.

Ведомость рабочих чертежей основного комплекта

Лист

Наименование

Примечание

1

Общие данные

2

План электроснабжения. М1:500

Ведомость ссылочных и прилагаемых документов

Обозначение

Наименование

Примечание

Прилагаемые документы

а) Ссылочные документы:

ПУЭ изд. 7

Правила устройства электроустановок

СП 256.1325800.2016

“Электроустановки жилых и общественных зданий”

Госстрой России

СП 76.13330.2016

“Электротехнические устройства”

Госстрой России

СП 52.13330.2016

“Естественное и искусственное освещение”

СанПиН 1.2.3685–21

“Гигиенические нормативы и требования к обеспечению безопасности и (или) безвредности для человека факторов среды обитания”

СП 6.13130.2013

“Системы противопожарной защиты. Электрооборудование.

Требования пожарной безопасности.”

ГОСТ Р 50571.5.4–2013

“Заземляющие устройства, защитные проводники и защитные проводники уравнивания потенциалов”

б) Прилагаемые документы:

Вновь выпущенные

11-П-2024-ЭС.СО

Спецификация оборудования, изделий и материалов

A12-2022

Прокладка кабелей с применением модульных кабельных колодцев

11-П-2024-ЭС.КЖ

Кабельный журнал

Технические решения принятые в рабочем проекте, соответствуют требованиям национальных стандартов Российской Федерации, действующим нормам и правилам проектирования объектов, требованиям охраны труда и промышленной безопасности, санитарно-гигиеническим, противопожарным и другим требованиям системы безопасности труда и обеспечивают безопасность для жизни людей эксплуатацию при соблюдении предусмотренных мероприятий.

Общие указания

Рабочие чертежи разработаны в соответствии с действующими нормами, правилами и стандартами. Рабочая документация разработана на основании:

- технического задания, утвержденного Заказчиком;
- согласованного генерального плана участка проектирования со свободным планом сетей;
- письма от Заказчика исх. №223 от 09.07.2024г.;

Приведенные в настоящем разделе технические решения электроснабжения и электроосвещения разработаны в соответствии с действующими на территории РФ Федеральными законами о технических регламентах, свободами правил и национальными стандартами (или частями стандартов), утвержденных Правительством Российской Федерации.

В соответствии с законом о сертификации РФ все указанные приборы, изделия, материалы и оборудование должны быть сертифицированы и иметь сертификаты соответствия и пожарной безопасности согласно установленным перечням.

Акты освидетельствования скрытых работ:

- прокладка ПНД труб в траншеях и устройство кабельных колодцев.

Данным проектом предусмотрены основные решения по прокладке ПНД труб для дальнейшего устройства резервных кабельных линий от входного кабельного колодца до проектируемых кабельных колодцев. ПНД трубы предусмотрены для устройства в дальнейшем кабельных линий для обеспечения резервирования существующих кабельных линий проложенных под площадью фиджیتال центра от внодь проектируемой ТП6/0,4 кВ до границы земельного участка по ул. Спортивная..

Для прокладки кабельных линий от входного кабельного колодца до точек подключения в проектируемых кабельных колодцах выбрана ПНД труба d200. Прокладку труб в земле выполнить по типовому проекту А11-2011.

Устройство кабельных колодцев выполнить согласно типового А12-2022.

Трубы в земле проложены на глубине 0,7 м от планировочной отметки. В местах пересечений с инженерными сооружениями и дорогами защищены жесткими двустенными гофрированными трубами d=200мм . Перед прокладкой труб выполнена подсыпка песка на дно траншеи, а сверху проложенные трубы засыпаны слоем мелко разрыхленной земли и песка. Радиусы изгиба труб не менее 800 мм.

Трубы под автодорогами и проездами проложен на глубине не менее 1,0 м от планировочной отметки земли.

Трубы для устройства взаимно резервируемых питающих К/Л прокладываются в одной траншее с разделением несгораемой перегородкой из полнотелого кирпича на расстоянии друг от друга 250мм согласно технического циркуляра №16/2007 и типового проекта А11-2011.

Заземление и защитные меры безопасности выполнены в соответствии с ПУЭ.

Все электромонтажные работы вести в соответствии с действующими ПУЭ, ПОТ Р М016-2001, РД 153-34.0-03.150-00.

39МЗ-Р-2024-ЭС.1

ПРОВЕДЕНИЕ РАБОТ ПО БЛАГОУСТРОЙСТВУ ТЕРРИТОРИИ (ЕЕ ЭЛЕМЕНТОВ) ДЛЯ СОЗДАНИЯ «УМНОЙ» СПОРТИВНОЙ ПЛОЩАДКИ

Изм

Колуч

Лист

№ док.

Подпись

Дата

Разработал

Бутенко

Проверил

Петров

07.24

07.24

Самарская область, г. Самара, железнодорожный район, ул. Спортивная: кадастровые номера участков 63:01:0104002:1115, 63:01:0104002:1117

Стадия

Лист

Листов

Р

1

Общие данные

Н.контр

Азова

ГИП

Зверобоев




07.24

07.24

Формат А3А

Спецификация					
Вариант	И				
Листы и дата					
Имя и подпись					

- Условные обозначения:
- граница земельного участка
 - проектируемое модульное здание фиджитал-центра
 - проектируемая зона волейбола
 - проектируемая зона стритбола (14x15) и пляжного волейбола
 - проектируемая зона Мини-футбола (поле 40x20)
 - ограждение участка
 - озеленение
 - элементы для демонтажа
 - тротуар
 - проектируемые сети наружного электроосвещения прокладываемые в земле
 - проектируемые сети наружного электроосвещения прокладываемые по модульному зданию фиджитал центра в трубе гофрированной ПВХ FRLS стойкой к УР
 - Пржектор светодиодный пятидиодный LADesign LAD LED R500-5-M-6-350 (1000), 220В, 350Вт, 49843/м, 5000К, 9Х/11, IP67. кл. заш. I крепление при помощи лиры к Т-образному кронштейну на опору Н-8м
 - Зная многофункциональная опора выполняется по отдельному проекту
 - Пржектор светодиодный пятидиодный LADesign LAD LED R500-4-M-6-300 (1000), 220В, 280Вт, 49280/м, 5000К, 9Х/11, IP67. кл. заш. I крепление при помощи лиры к Т-образному кронштейну на опору Н-8м
 - Пржектор светодиодный LADesign LAD LED R500-1-M-6-35 (1000), 220В, 35Вт, 5502/м, 5000К, 9Х/11, IP67. кл. заш. I крепление при помощи лиры к фасаду здания фиджитал центра

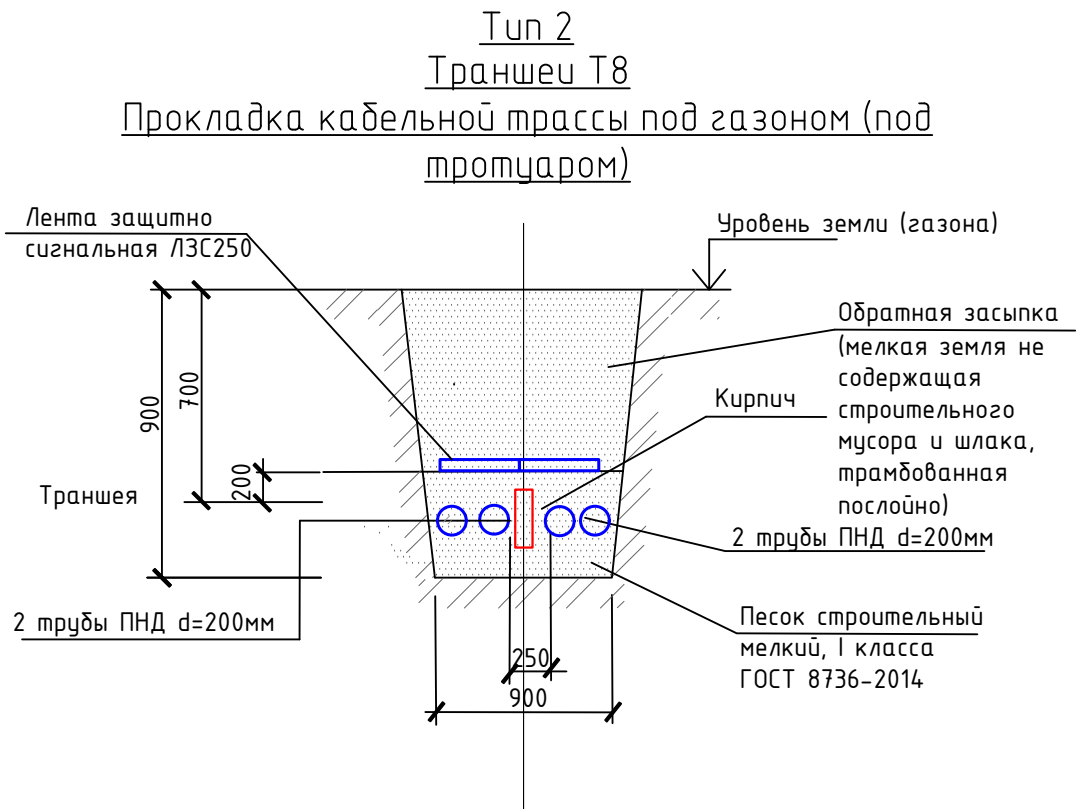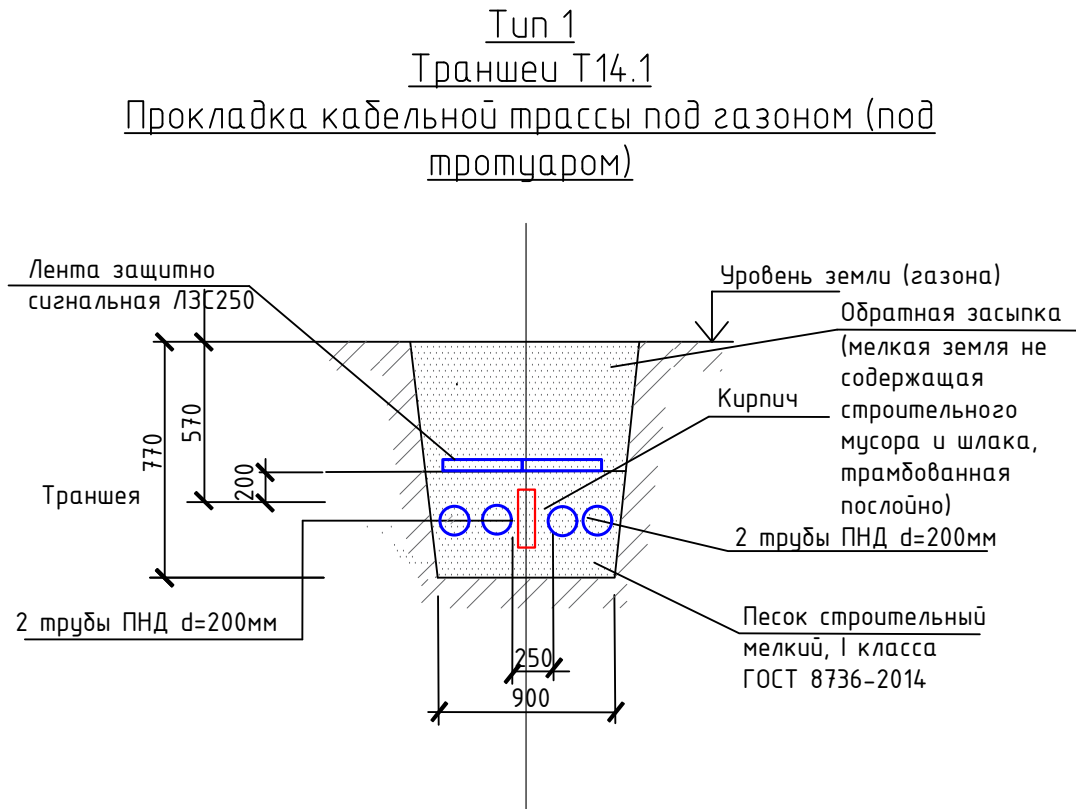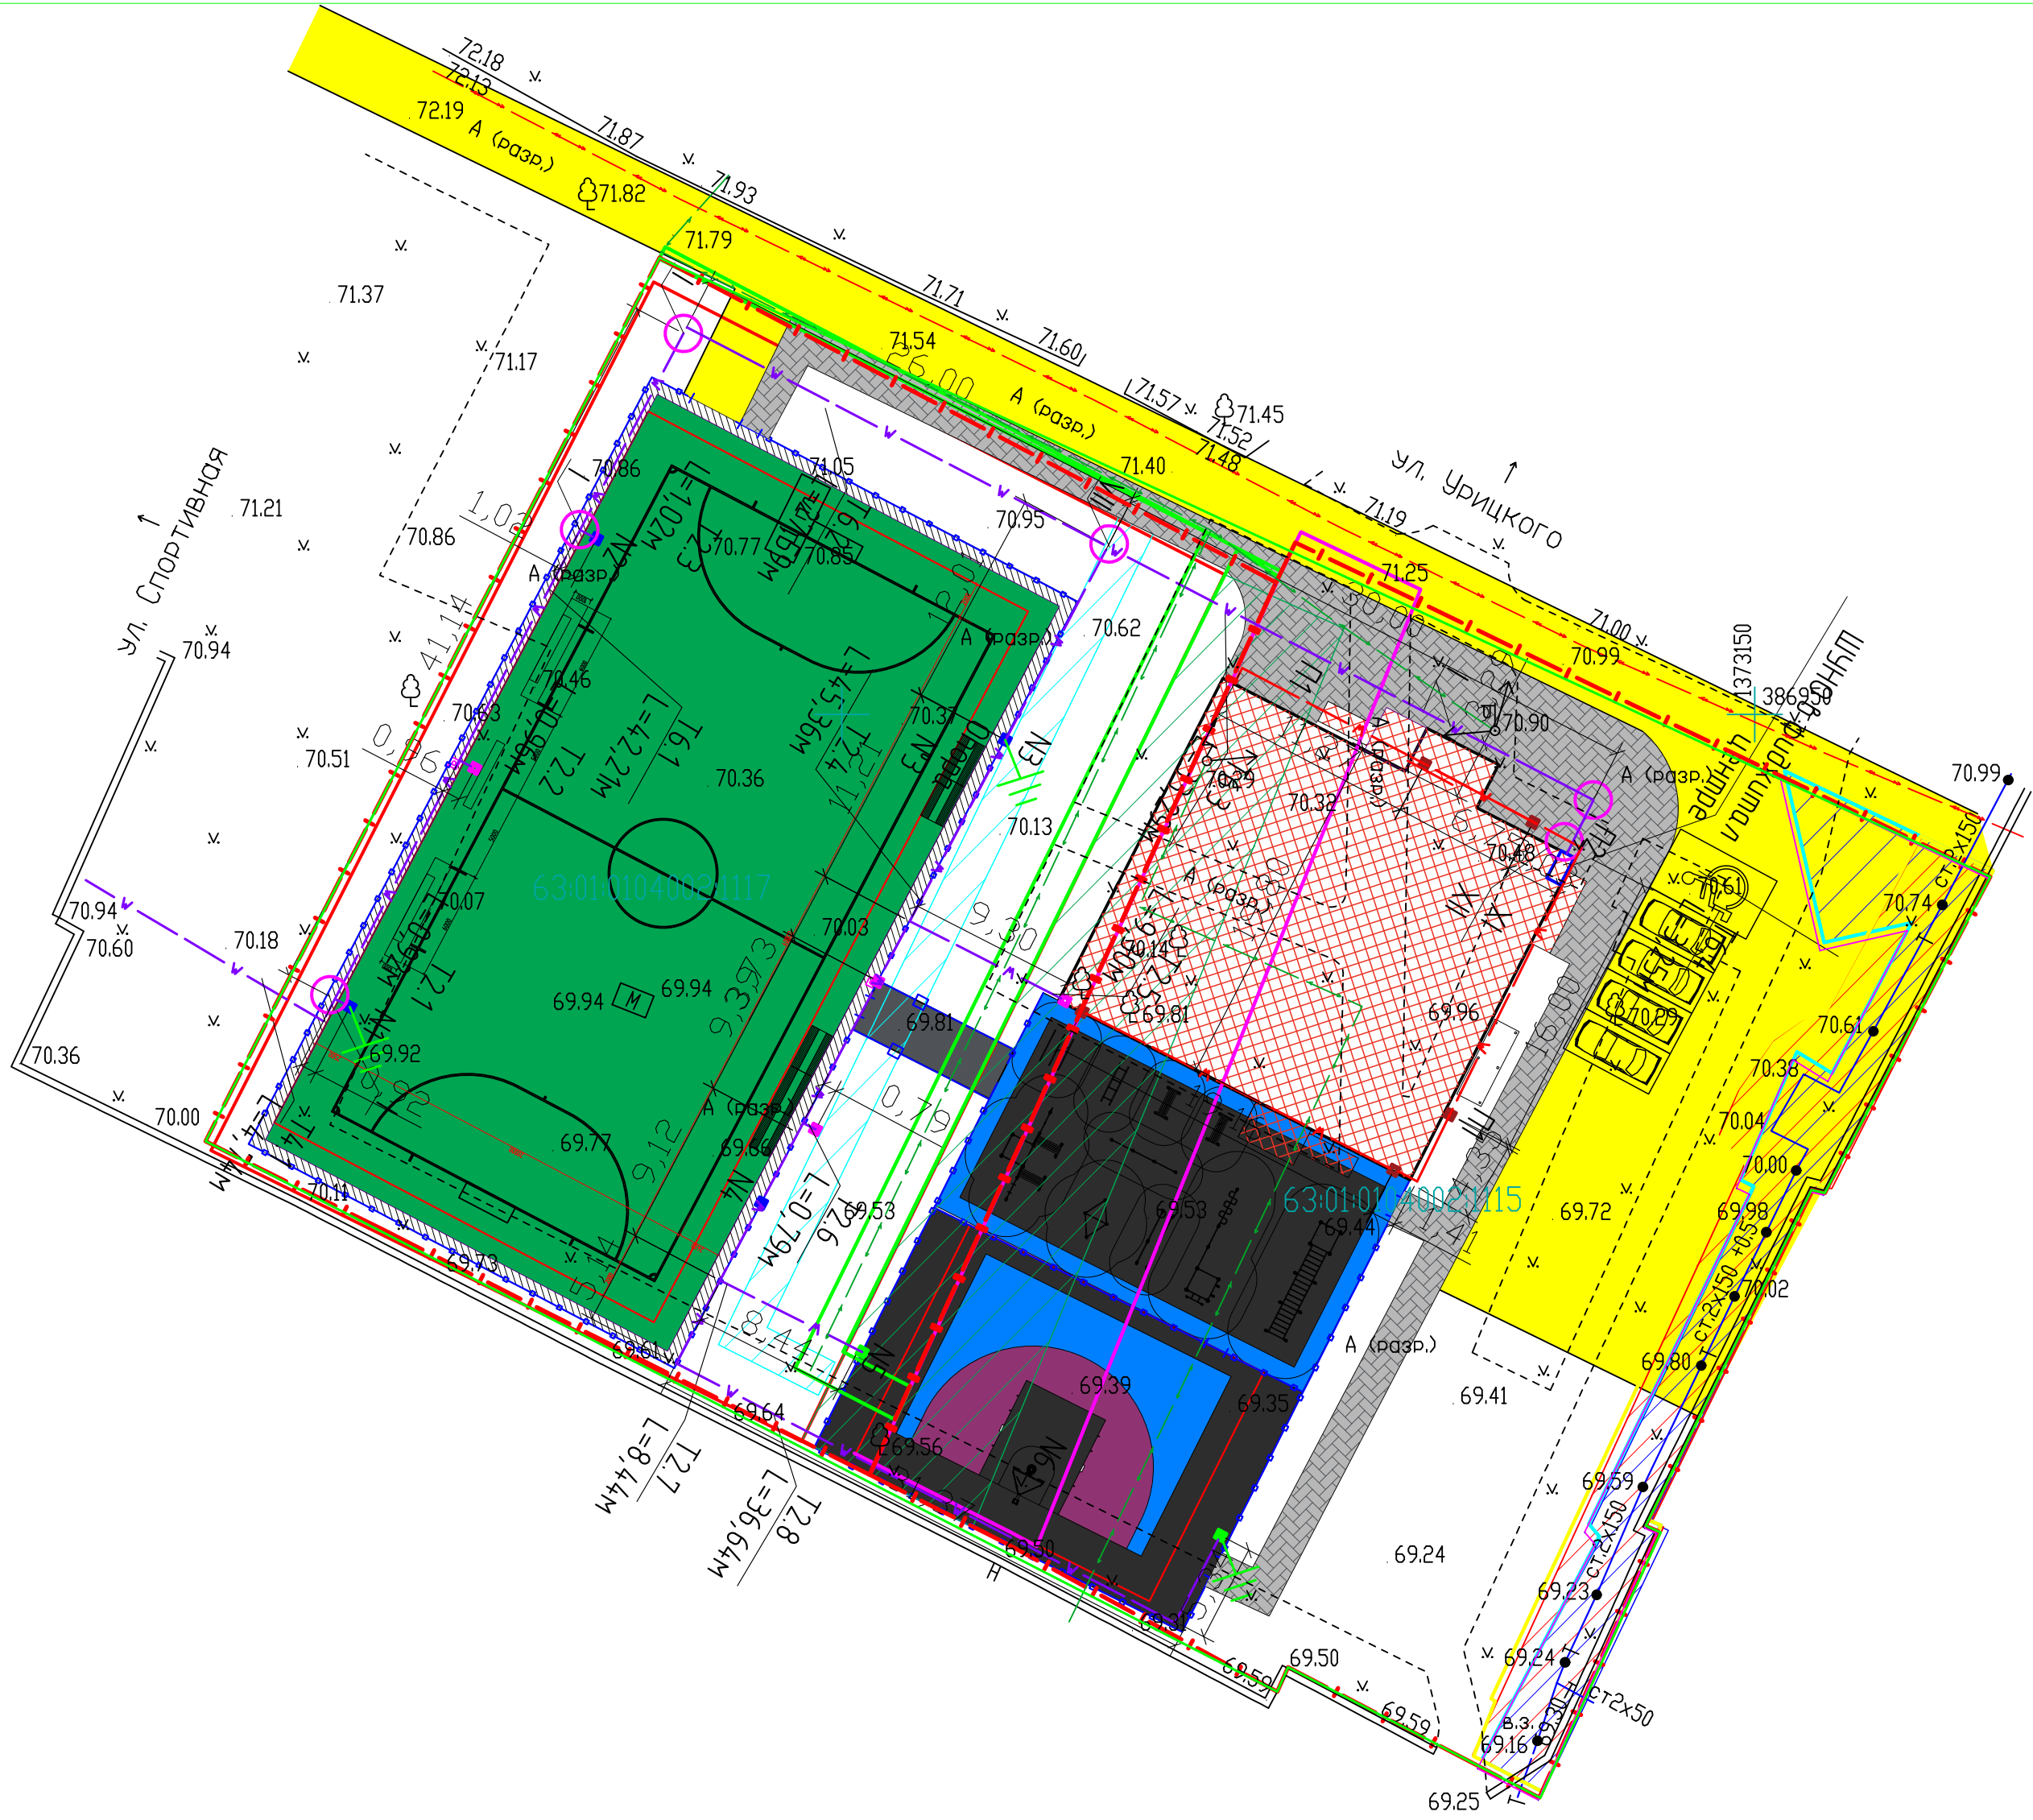

- Примечания
- 1 В рамках данного комплекта рассматривается устройство ПНД для дальнейшей прокладки резервных кабельных линий от проектируемого колодца на границе участка колодца до проектируемых колодцев внутри площадки для кабельных линий ААШВ 4х150 прокладываемых под площадью фиджитал центра от проектируемой ТП 6/0,4кВ до краев участка.
 - 2 Данные трубы ПНД позволяют осуществить устройство кабельных линий в случае аварийной ситуации. Поставка, затягивание и устройство непосредственно кабелей в трубе осуществляется по отдельному проекту.
 - 3 Трубы ПНД для устройства в дальнейшем кабельных линий применены с протяжкой d=200мм
 - 4 В период устройства кабельных линий за границей участка проектирования необходимо выполнить демонтаж и восстановление благоустройства территории (асфальтобетонного покрытия проездов и проходов).
 - 5 Объем земляных работ для устройства колодцев
 - разработка грунта для посадочной ямы - 47,4 куб.м.
 - обратная засыпка песком, включая организацию песчаной подушки 300мм - 39,6 куб.м.

Экспликация траншей						
№ поз.	Наименование	Тип (исполнение)	№ чертежа	Ед. измер.	Кол-во	Примечание
I	Минимальные радиусы изгиба труб при прокладке		A11-2011.09	Дн	15	
II	Минимальные расстояния между параллельно прокладываемыми трубами		A11-2011.12	м	0,25	
III	Габариты кабельных траншей и объемы земляных работ		A11-2011.13	м	49,86	
IV	Защита кабелей от механических повреждений		A11-2011.15	м	49,86	траншеи Т8, Т14
V	Прокладка кабельной линии параллельно с трубопроводом		A11-2011.17	м	-	
VI	Прокладка кабельной по отношению к деревьям и кустарникам		A11-2011.27	м	-	
VII	Пересечение двух кабельных линий в земле		A11-2011.29	шт	-	
VIII	Пересечение кабелей с трубопроводом		A11-2011.31	шт	-	
IX	Пересечение кабелей с теплопроводом		A11-2011.32	шт	-	
X	Прокладка кабельной линии открытым способом при пересечении с автодорогой		A11-2011.38	шт	-	
XI	Уплотнение кабеля в трубе		A11-2011.43	шт	-	
XII	Ввод кабельной линии в здание или кабельное сооружение. Вариант Э		A11-2011.46	шт	-	

Объем земляных работ											
Траншея	Габариты траншеи				Объемы земляных работ						Длина траншеи в проекте, м d=90
	Длина, м	Ширина низа траншеи, м	Ширина верха траншеи, м	Глубина, м	Рытье, куб.м	Основание под кабели, песок куб.м	Обваловка, песок куб.м	Обратная засыпка, грунт куб.м	Кирпич, шт	Сигнальная лента, м	
Электрооснаждение 0,4кВ											
Т14.1	12,61	0,9	1,0	0,77	9,2	1,2	2,4	5,6	51	37,83	50,44
Т8.1	47,25	0,9	1,0	0,9	40,4	4,25	8,51	27,64	225	141,75	189,0
ИТОГО (по таблице)	49,86	-	-	-	49,6	5,45	10,91	33,24	276	179,58	199,4

						39МЗ-Р-2024-ЭС.1		
						ПРОВЕДЕНИЕ РАБОТ ПО БЛАГОУСТРОЙСТВУ ТЕРРИТОРИИ (ЕЕ ЭЛЕМЕНТОВ) ДЛЯ СОЗДАНИЯ «УМНОЙ» СПОРТИВНОЙ ПЛОЩАДКИ		
Изм.	Колуч.	Лист	№ док	Подпись	Дата	Самарская область, г. Самара, железнодорожный район, ул. Спортивная; кадастровые номера участков 63:010104002.115, 63:010104002.117	Стодия	Листов
Разработал	Буленко				07.24		Лист	Листов
Проверил	Петров				07.24	участков 63:010104002.115, 63:010104002.117		
И.контр.	Азова				07.24	План электрооснащения. М1500		
ГИП	Зверовоев					sitronics GROUP		

Кабельный журнал

[illegible]

1 Длина кабельной продукции указана с учетом 20% на изгибы, повороты, "змеёвку" и провис

						39МЗ-Р-2024-ЭС.1.КЖ			
						ПРОВЕДЕНИЕ РАБОТ ПО БЛАГОУСТРОЙСТВУ ТЕРРИТОРИИ (ЕЕ ЭЛЕМЕНТОВ) ДЛЯ СОЗДАНИЯ «УМНОЙ» СПОРТИВНОЙ ПЛОЩАДКИ			
Изм.	Колуч	Лист	№ док.	Подпись	Дата				
Разработал	Бутенко				07.24	Самарская область, г. Самара, железнодорожный район, ул. Спортивная: кадастровые номера участков 63:01:0104002:115, 63:01:0104002:1117	Стадия	Лист	Листов
Проверил	Петров				07.24		Р	1	
Н.контр	Азова				07.24	Кабельный журнал			
ГИП	Зверобоев								