

Свидетельство о допуске к определенному виду работ, которые оказывают влияние на безопасность объекта капитального строительства № 0073.03-2017-7735116621-П-163 от 11.05.2017

**ПРОВЕДЕНИЕ РАБОТ ПО БЛАГОУСТРОЙСТВУ ТЕРРИТОРИИ
(ЕЕ ЭЛЕМЕНТОВ) ДЛЯ СОЗДАНИЯ «УМНОЙ» СПОРТИВНОЙ ПЛОЩАДКИ
ПО АДРЕСУ:**

**КАДАСТРОВЫЕ НОМЕРА УЧАСТКОВ: 63:01:0104002:1115,
63:01:0104002:1117.**

**САМАРСКАЯ ОБЛАСТЬ, Г. САМАРА, ЖЕЛЕЗНОДОРОЖНЫЙ РАЙОН, УЛ.
СПОРТИВНАЯ.**

РАБОЧАЯ ДОКУМЕНТАЦИЯ

Раздел КР «Конструктивные решения»

8-25-КР

Изм.	№ док.	Подп.	Дата

Свидетельство о допуске к определенному виду работ, которые оказывают влияние на безопасность объекта капитального строительства № 0073.03-2017-7735116621-П-163 от 11.05.2017

**ПРОВЕДЕНИЕ РАБОТ ПО БЛАГОУСТРОЙСТВУ ТЕРРИТОРИИ
(ЕЕ ЭЛЕМЕНТОВ) ДЛЯ СОЗДАНИЯ «УМНОЙ» СПОРТИВНОЙ ПЛОЩАДКИ
ПО АДРЕСУ:
КАДАСТРОВЫЕ НОМЕРА УЧАСТКОВ: 63:01:0104002:1115,
63:01:0104002:1117.
САМАРСКАЯ ОБЛАСТЬ, Г. САМАРА, ЖЕЛЕЗНОДОРОЖНЫЙ РАЙОН, УЛ.
СПОРТИВНАЯ.**

РАБОЧАЯ ДОКУМЕНТАЦИЯ

Раздел КР «Конструктивные решения»

8-25-КР

Изм.	№ док.	Подп.	Дата


Взам. инв. №	
Подп. и дата	
Инв. № подл.	

Директор департамента



Анисимов И.В.


Главный инженер проекта

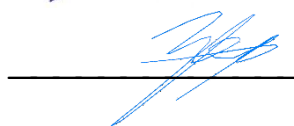

Зверобоев О.Л.

2025

Геолого-литологический разрез по линии II - II
М Г 1:500
В 1:100

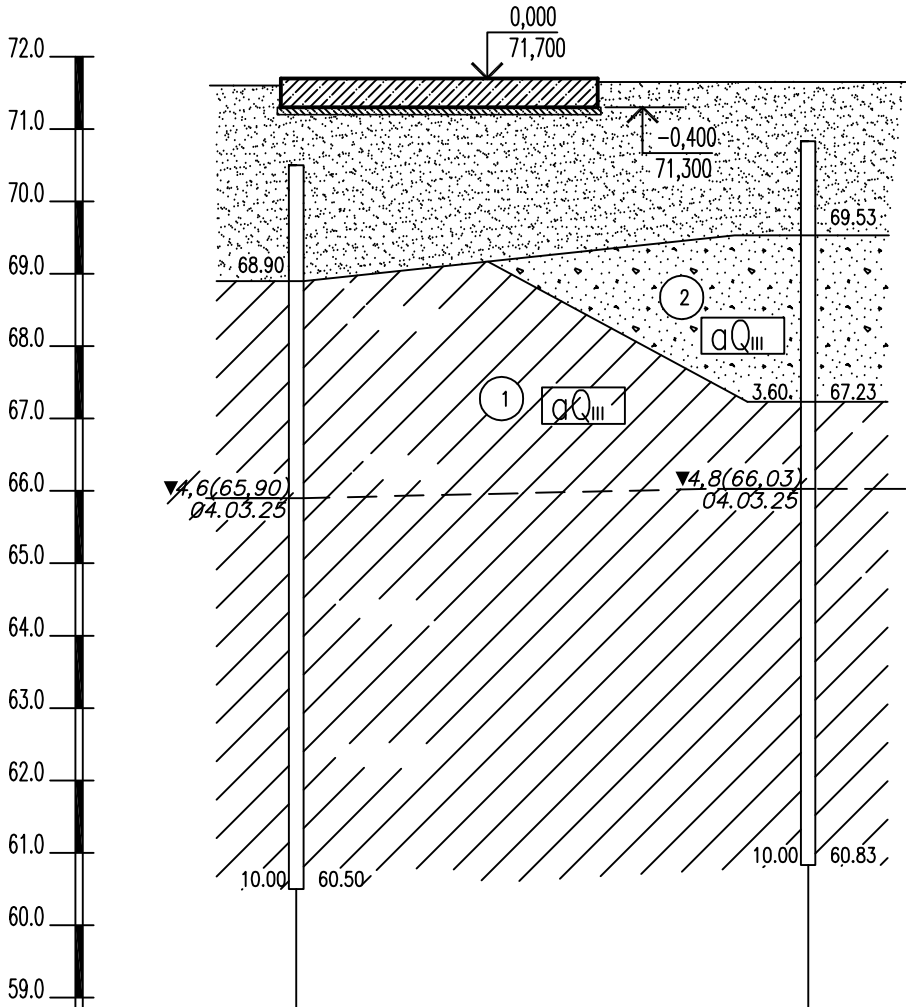

Номер скважины	Скв.4	Скв.2
Отметка устья, м	70,50	70,83
Расстояние, м	35.50	

Условные обозначения
Литология

- Песчаная подушка
- аQIII 1 Суглинок полутвердый
- аQIII 2 Песок плотный пылеватый

Буровая скважина
слева— глубина залегания подошвы ИГЭ, м

2.4
▼3.0(228.53)
18.02.21

в числителе— глубина установившегося уровня подземных вод, м (абс. отметка)
в знаменателе — дата замера
величина напора

10.0

справа— абс. отметка забоя скважины, м.

1 номер ИГЭ, слоя

— — — линия грунтовых вод


1. Абсолютная отметка уровня верха фундаментной плиты Фп-1 равная 71.700, условно принята за отметку 0.000.

Согласовано

Инв. N подл.	Взам. инв. N
Погр. и дата	


						8-25-КР			
						Устройство модульного спортивного сооружения по адресу: Самарская область, г.о. Самара, Железнодорожный район, ул. Спортивная, на территории земельных участков с кадастровыми номерами 63:01:0104002:1115, 63:01:0104002:1117			
Изм.	Кол. уч.	Лист	N док.	Погр.	Дата	Конструктивные решения	Стация	Лист	Листов
Разраб.		Кудашкина			06.25		Р	1	
Н.контр.		Шурыгин			06.25	Схема посадки фундаментной плиты на геолого-литологический разрез	ООО "КПСР"		
ГИП		Нефедова			06.25				

Схема расположения фундаментных плит

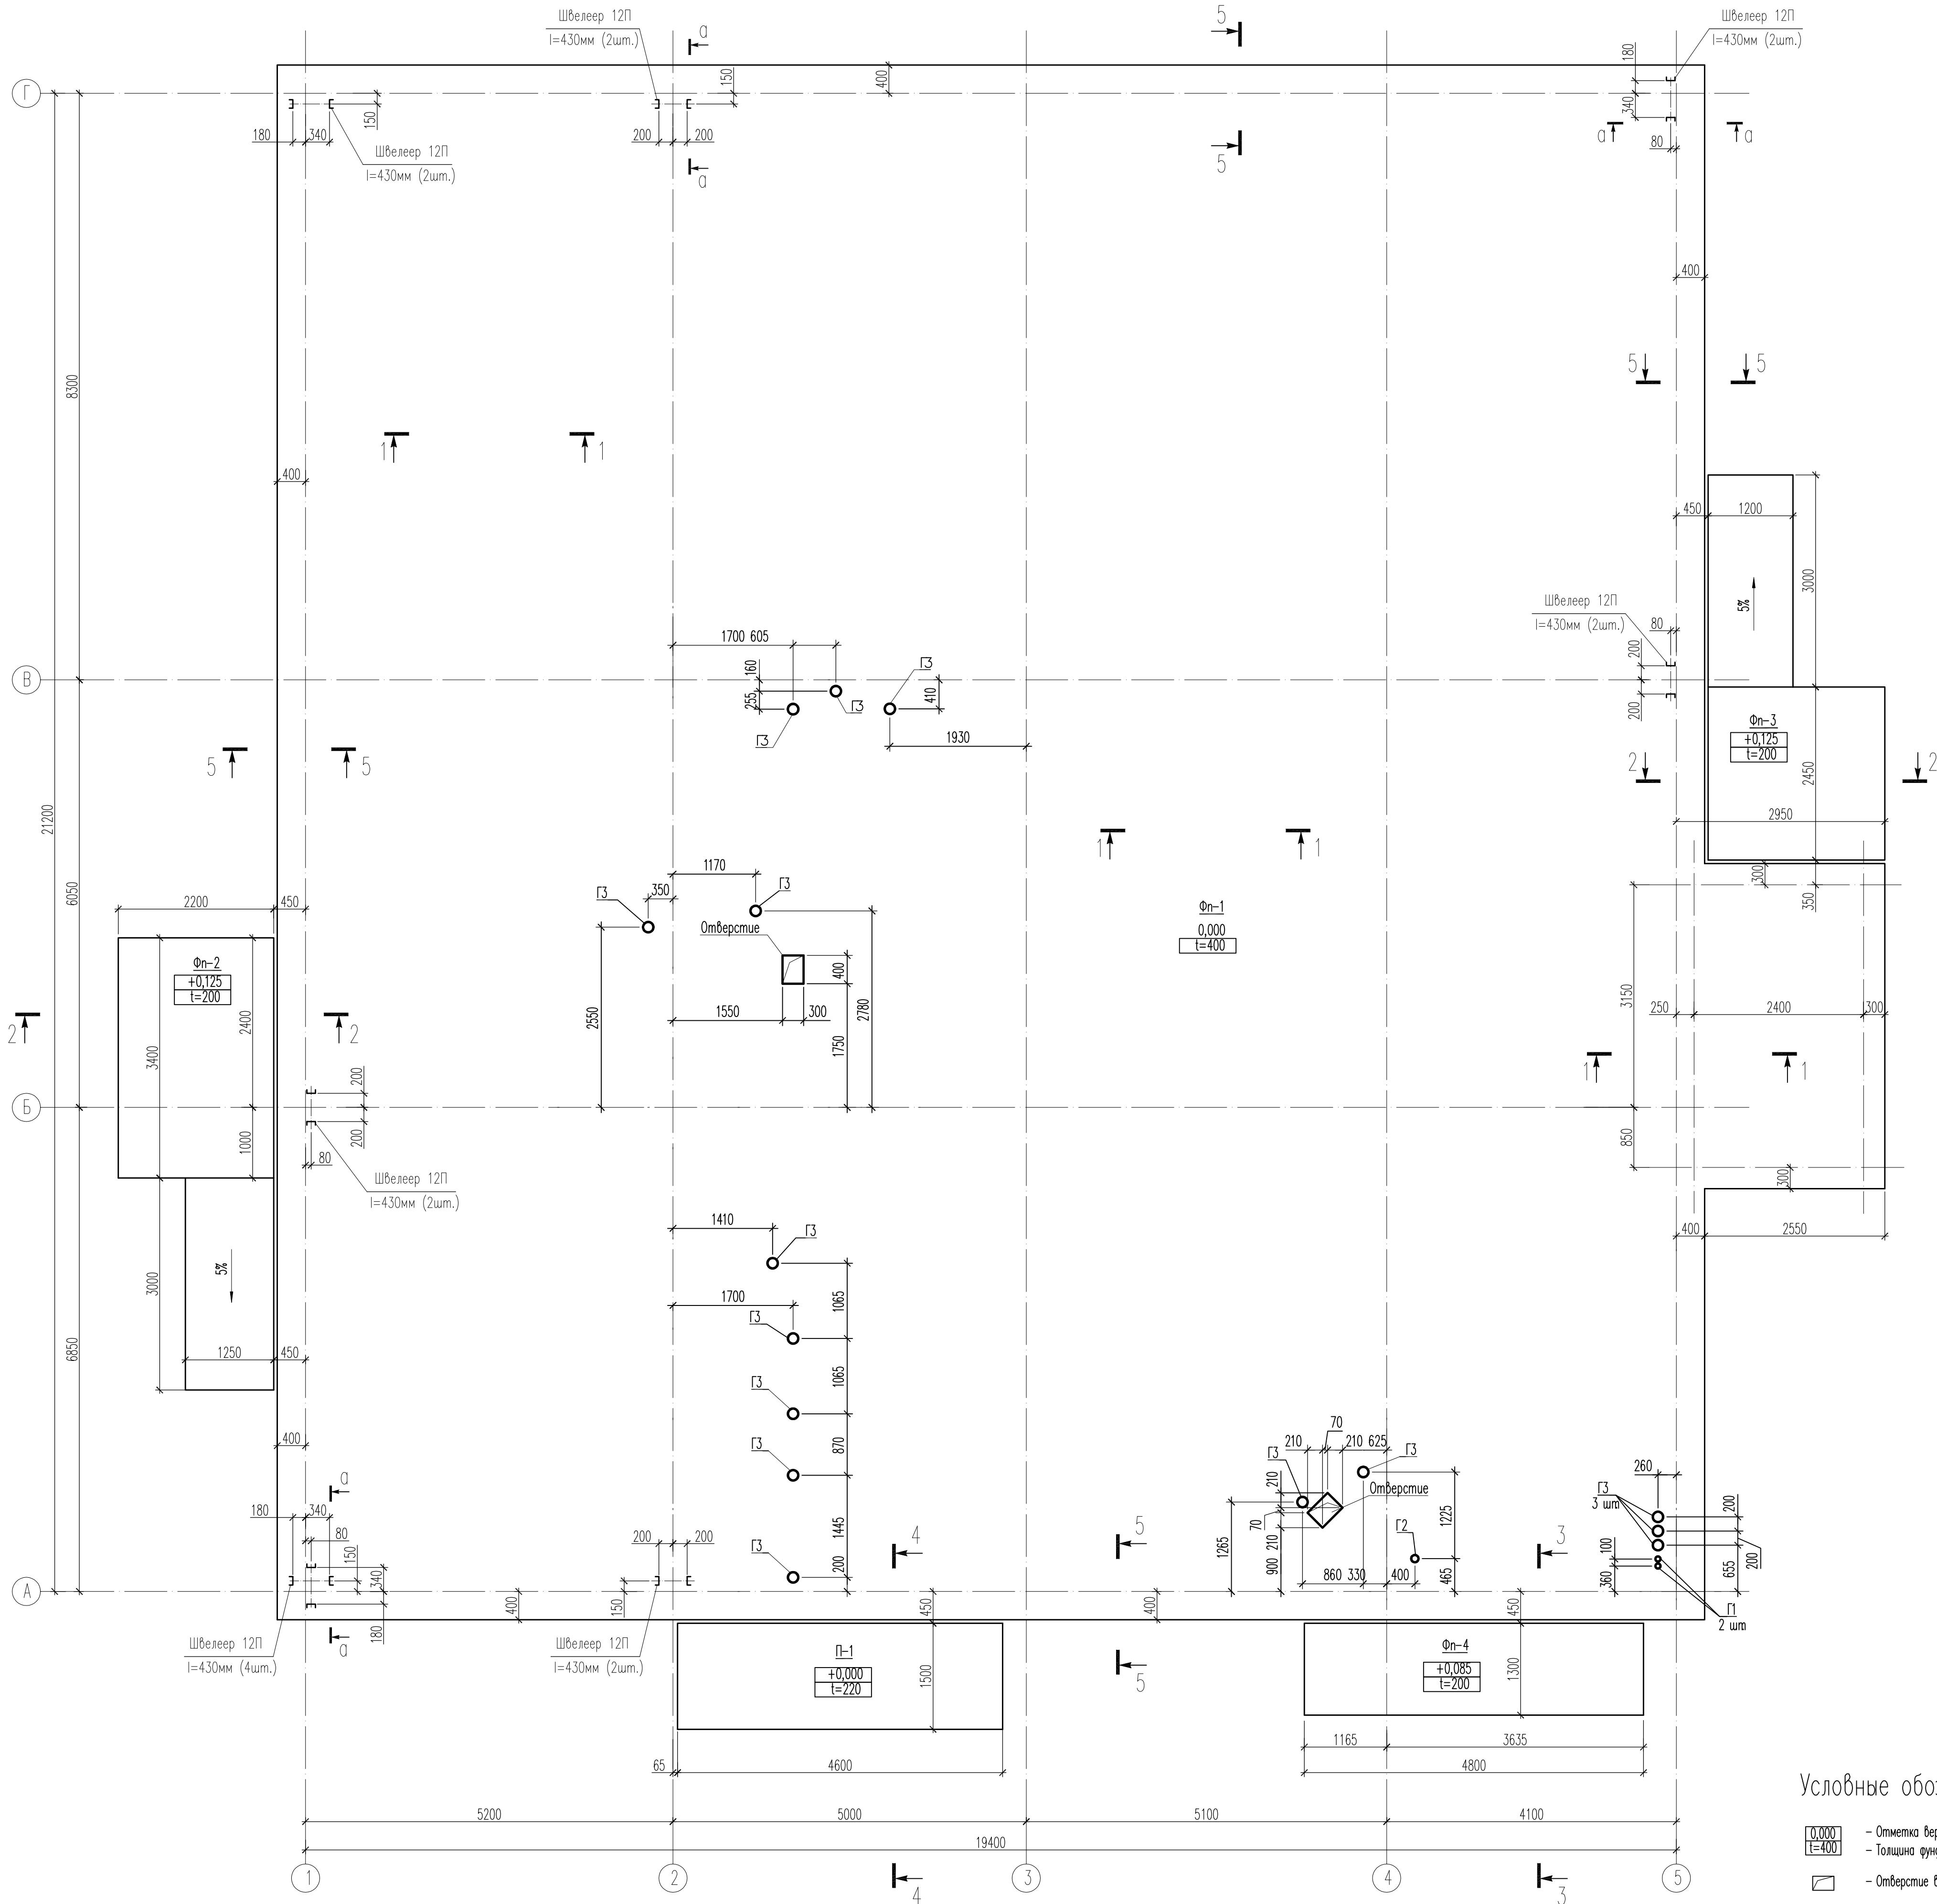

Спецификация к схема расположения фундаментных плит

Поз.	Обозначение	Наименование	Кол.	Масса ед.кг	Приме- чание
Фундаментные плиты					
Фн-1	см. лист 4	Плита фундаментная Фн-1	1		
Фн-2	см. лист 5	Плита фундаментная Фн-2	1		
Фн-3	см. лист 5	Плита фундаментная Фн-3	1		
Фн-4	см. лист 5	Плита фундаментная Фн-4	1		
П-1	ГОСТ 9561-2016	Плита сборная ПК 46.15-8 1	1	2170	
	С245 ГОСТ 27772-2015	Швеллер 12П ГОСТ 8240-97 Лобш.	7		мл.
Г-1		Труба 76х3 ГОСТ 10704-91 оцинк. L=920	2	5.0	
Г-2		Труба 108х4 ГОСТ 10704-91 оцинк. L=920	1	9.5	
Г-3		Труба 159х4 ГОСТ 10704-91 оцинк. L=920	15	14.1	
		Пеноплекс "Фундамент" 50 мм	36		м2
		Керамогранитная плитка 10 мм	36		м2

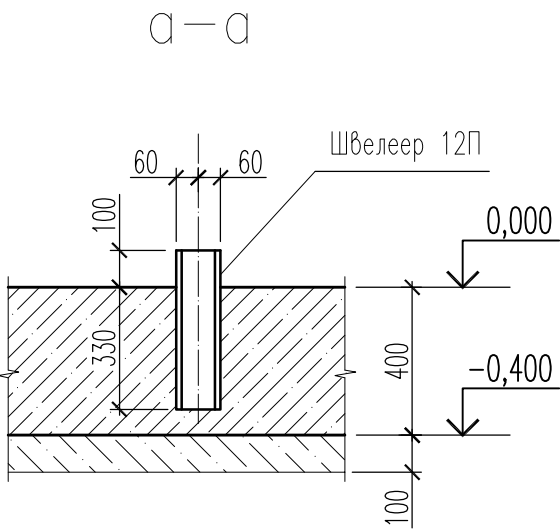


1. Абсолютная отметка урбана верха фундаментной плиты Фн-1 равная 71.700, условно принята за отметку 0.000.
2. В качестве фундаментных болтов приняты химические анкеры Nitli HIT-RE100 в комплекте с анкерными шпильками M24 HIT-V или эквивалент (96 шт.). Глубина анкеробки 330 мм.
3. Сечения 1-1 – 5-5 см. лист 3.

Условные обозначения


- 0.000 - Отметка верха фундаментной плиты
t=400 - Толщина фундаментной плиты, мм
□ - Отверстие в фундаментной плите

						8-25-КР		
						Устройство модульного спортивного сооружения по адресу: Самарская область, г.о. Самара, Железнодорожный район, ул. Спортивная, на территории земельных участков с кадастровыми номерами 63:01:0104002:1115, 63:01:0104002:1117		
Изм.	Кол. уч.	Лист	№ док.	Подп.	Дата	Конструктивные решения		
Разраб.	Кудашкина	А.И.	06.25					
						Стация	Лист	Листов
						Р	2	
Н.контр.	Шурягин	И.И.	06.25			Схема расположения фундаментных плит		
ГИП	Нефедова	И.И.	06.25					
						ООО "КПСР"		


1-1

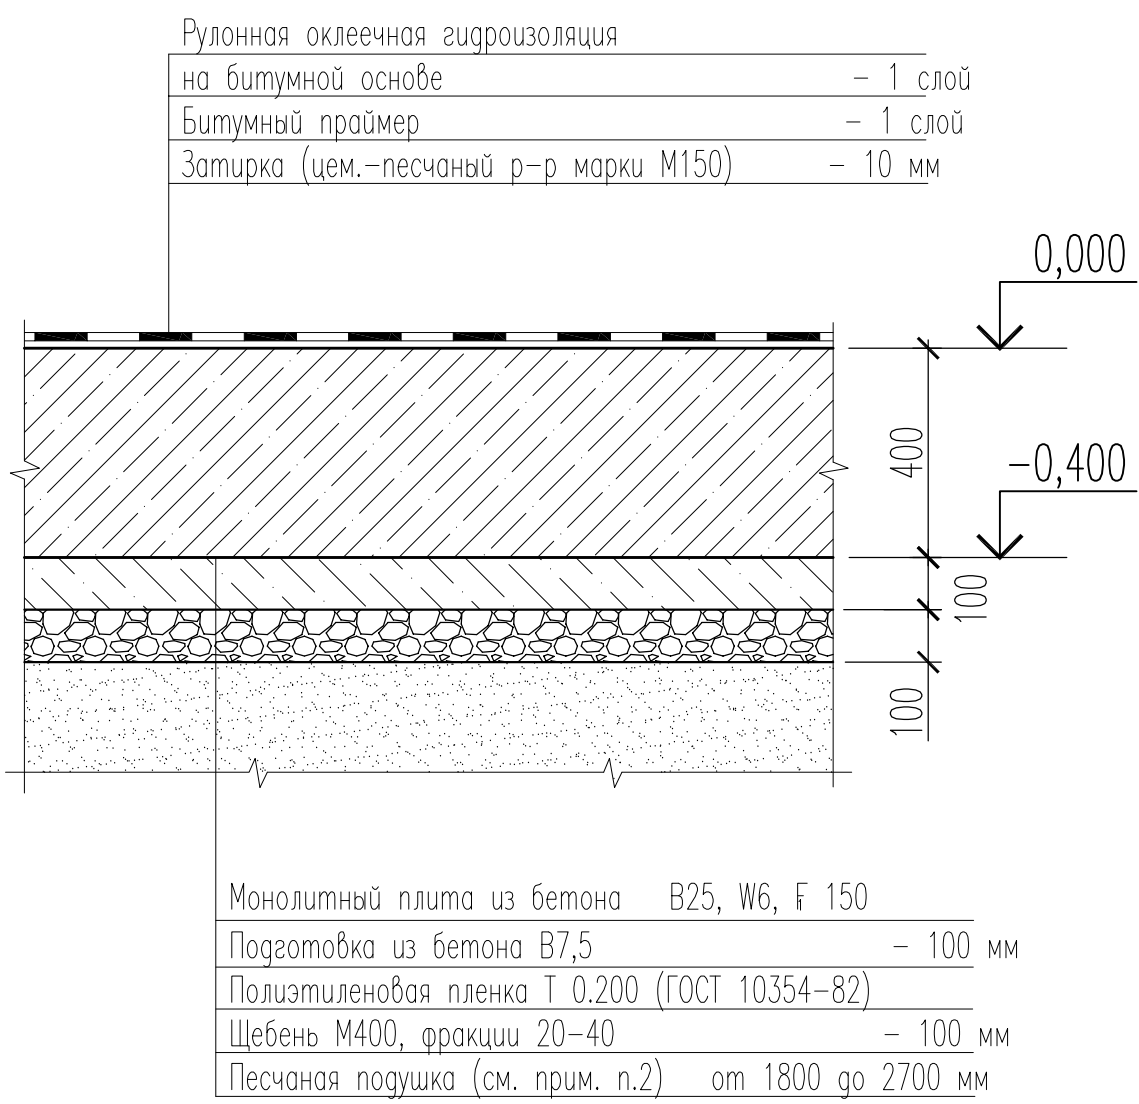


2-2

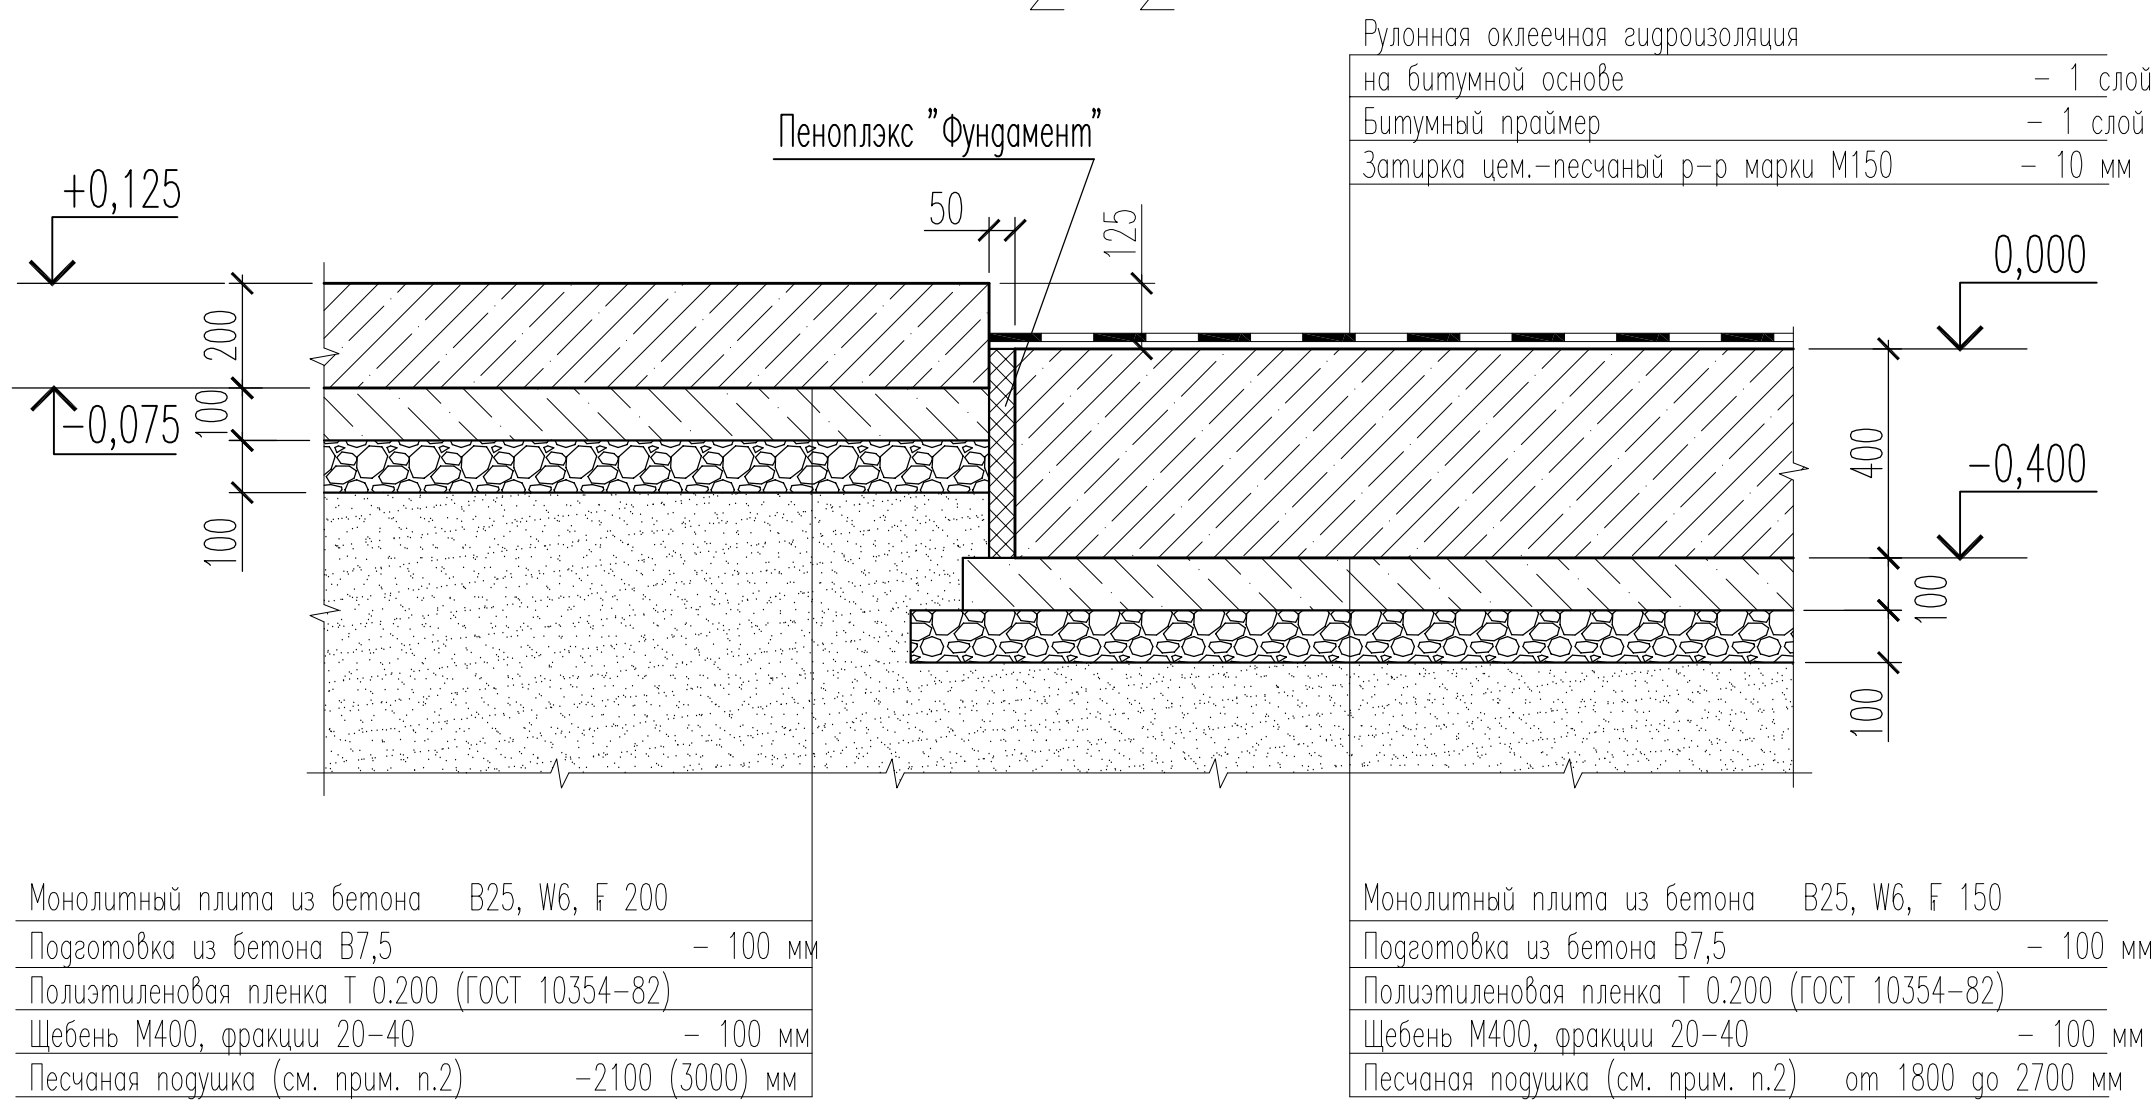


Узел проходки гильз "Г"

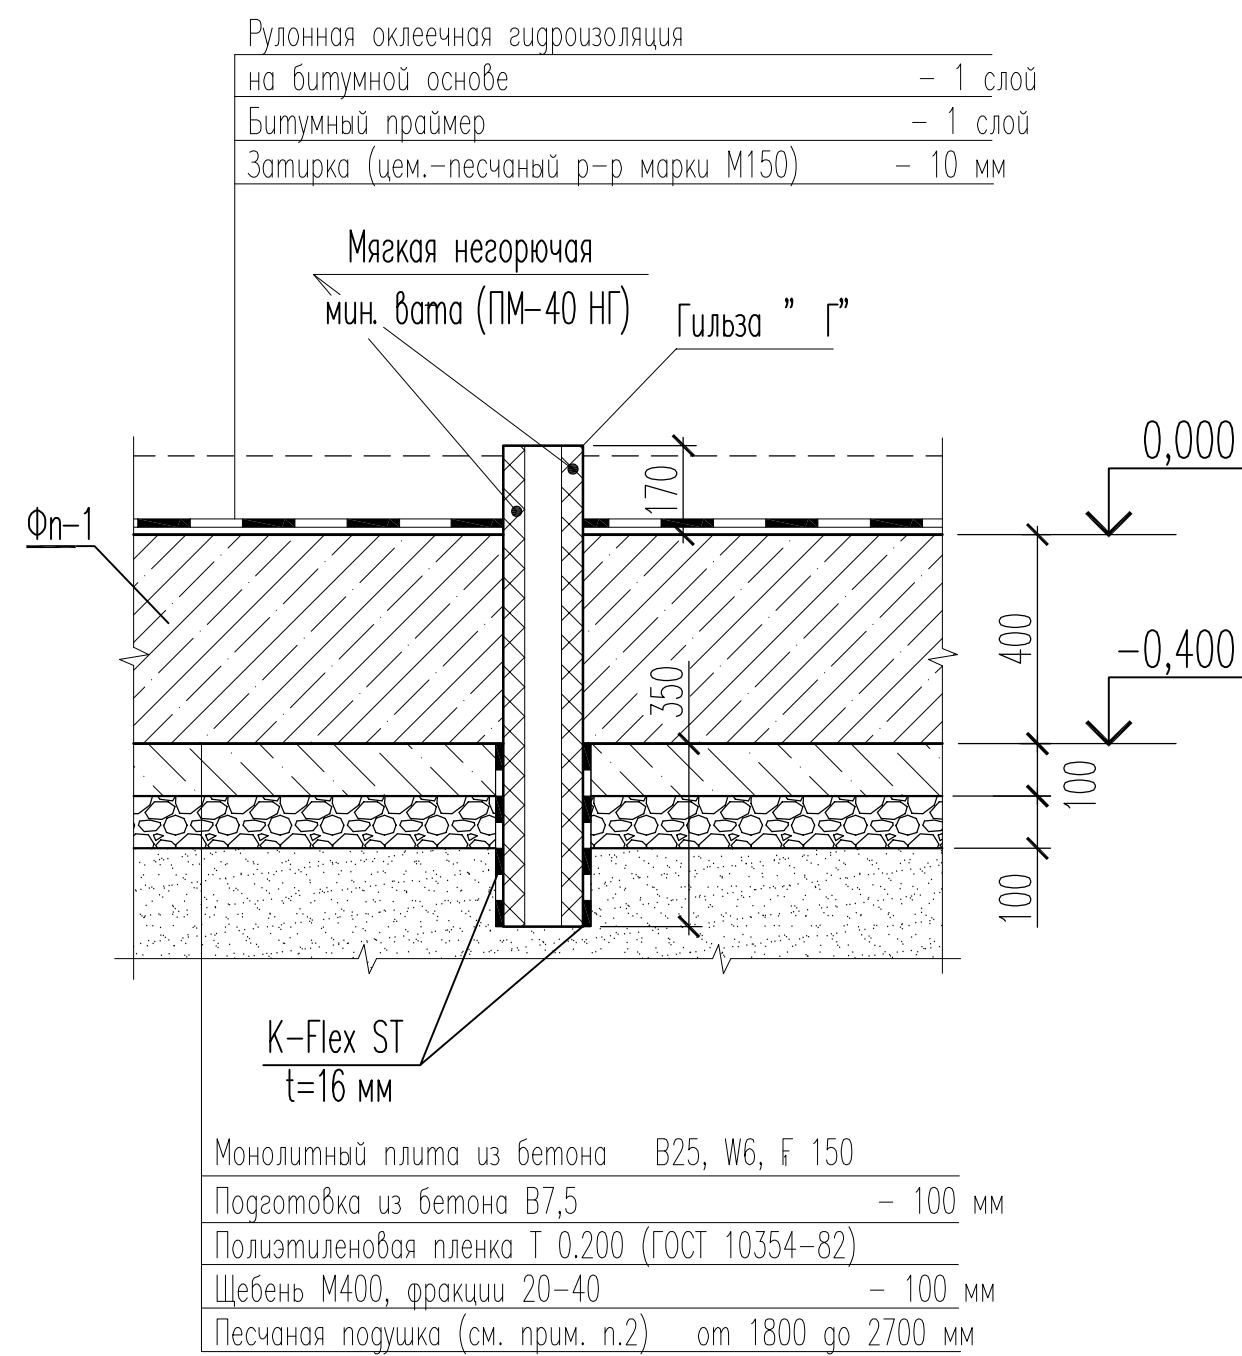


3-3

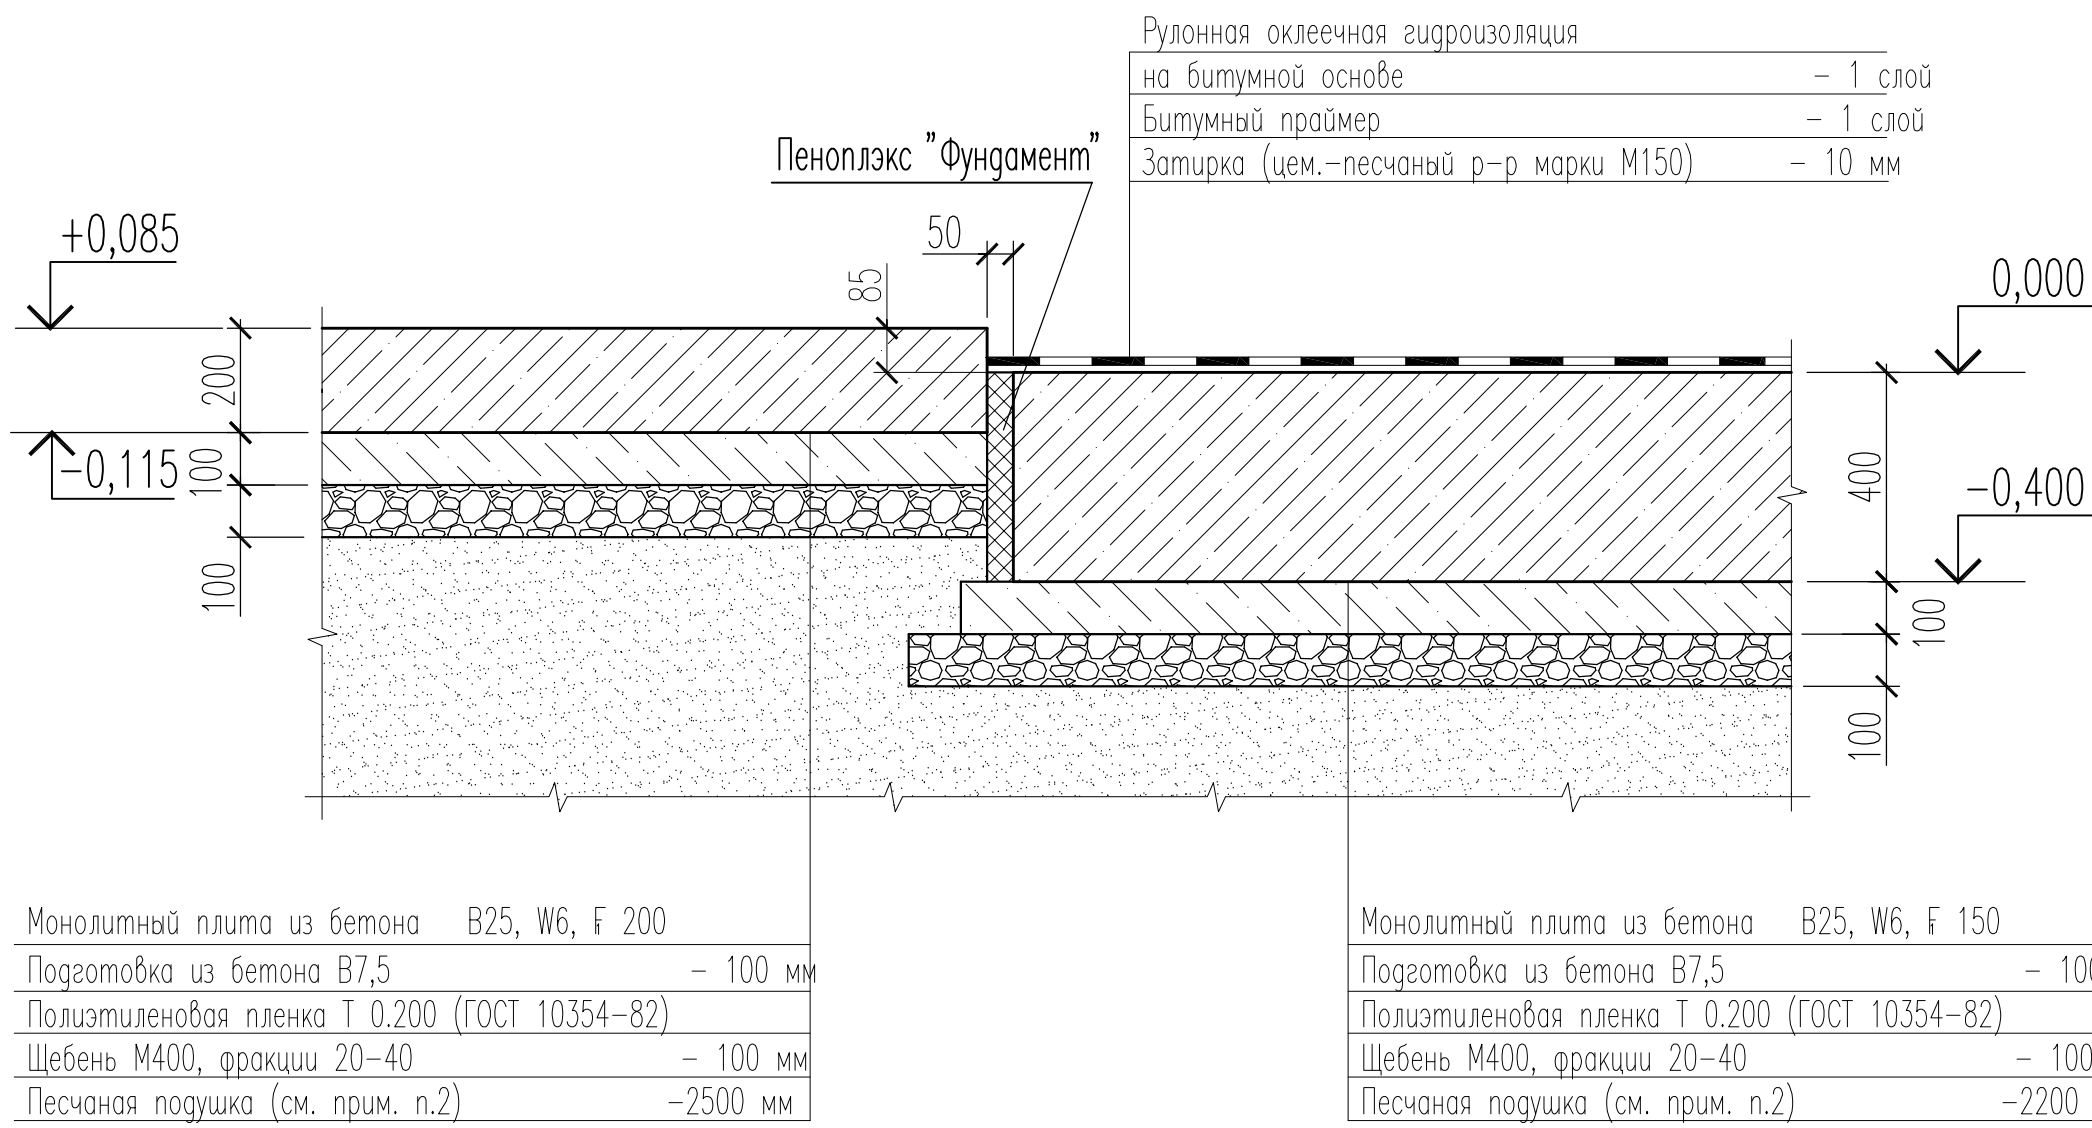

4-4

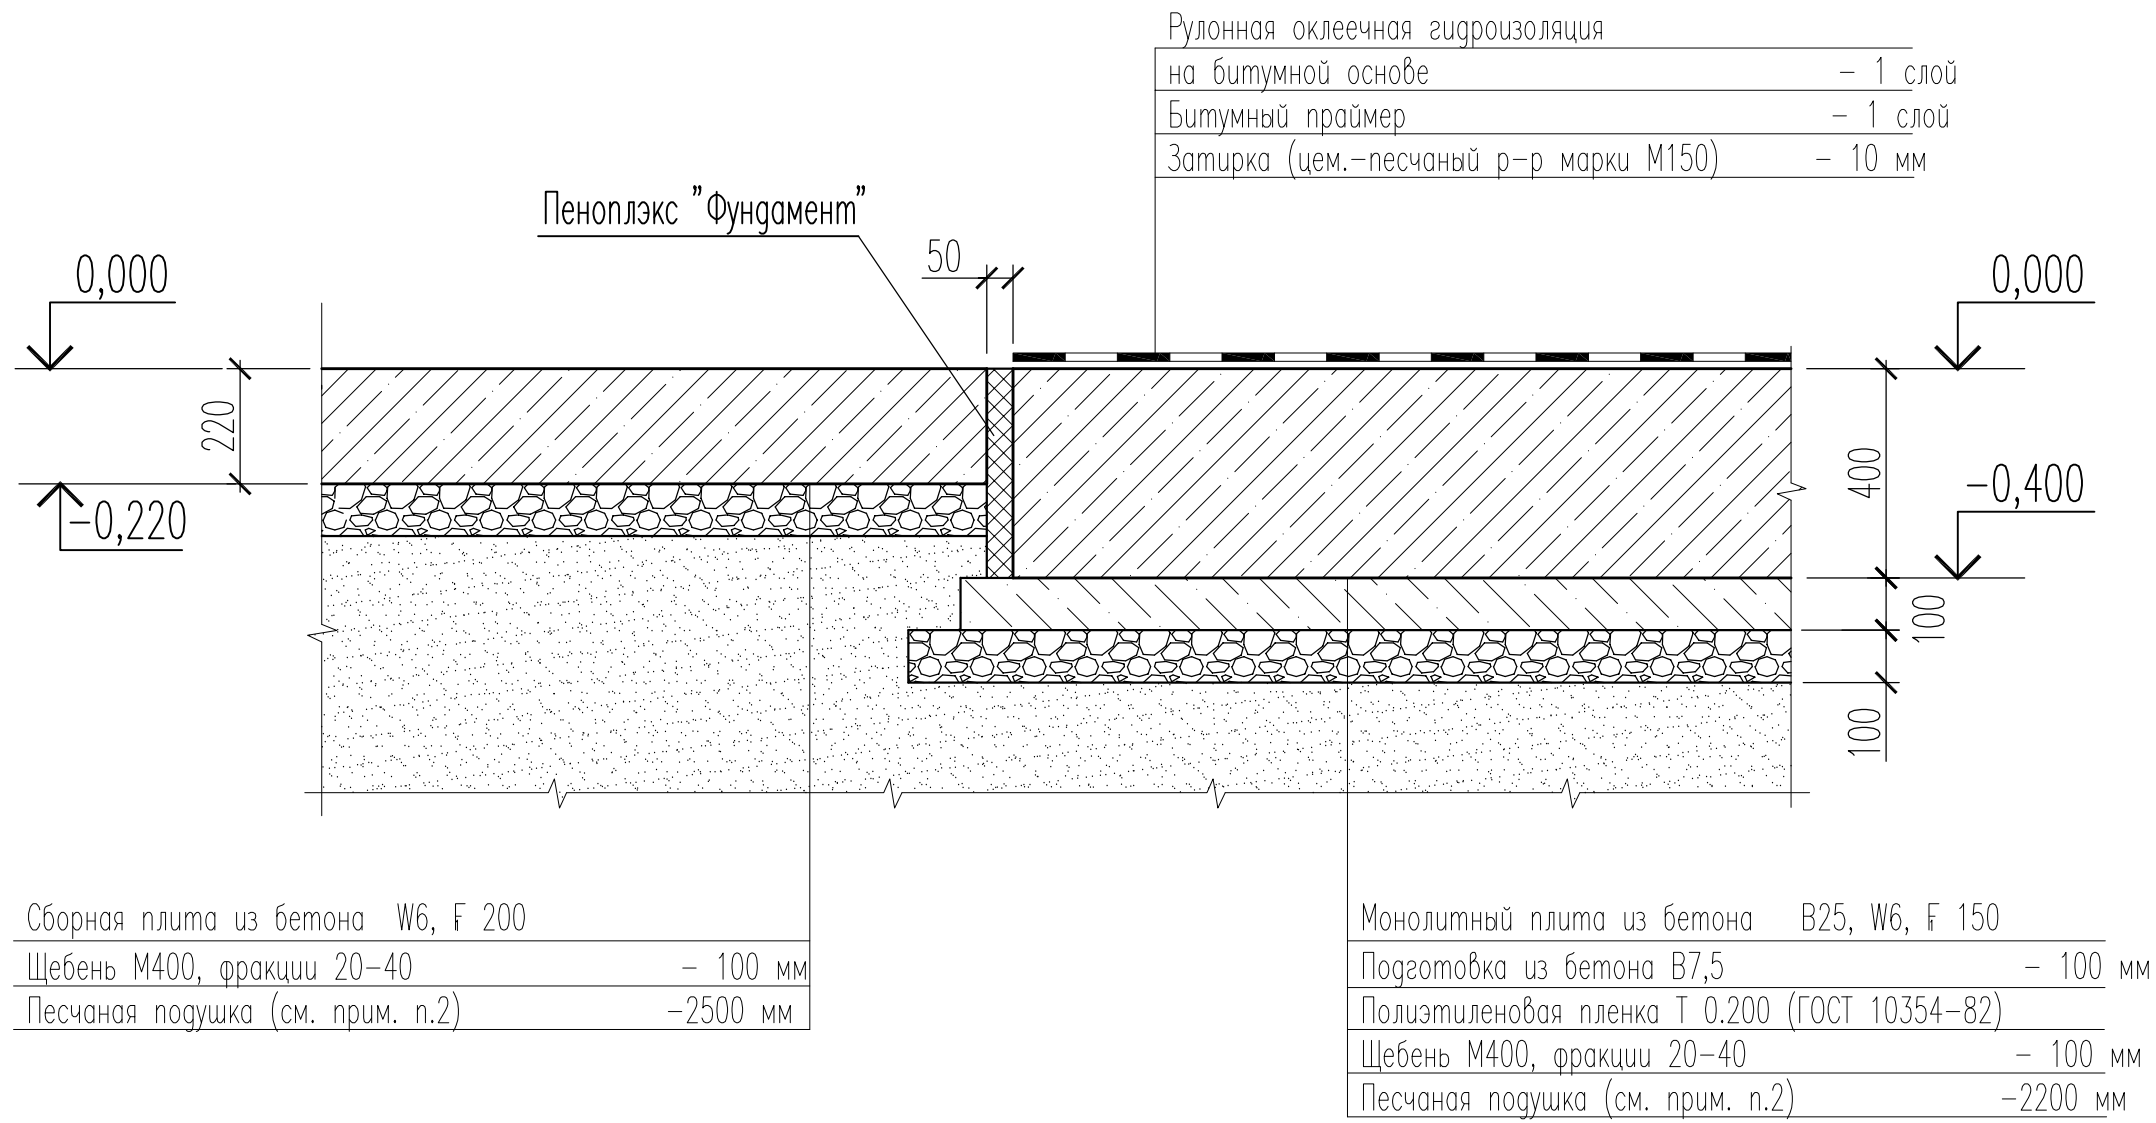

5-5

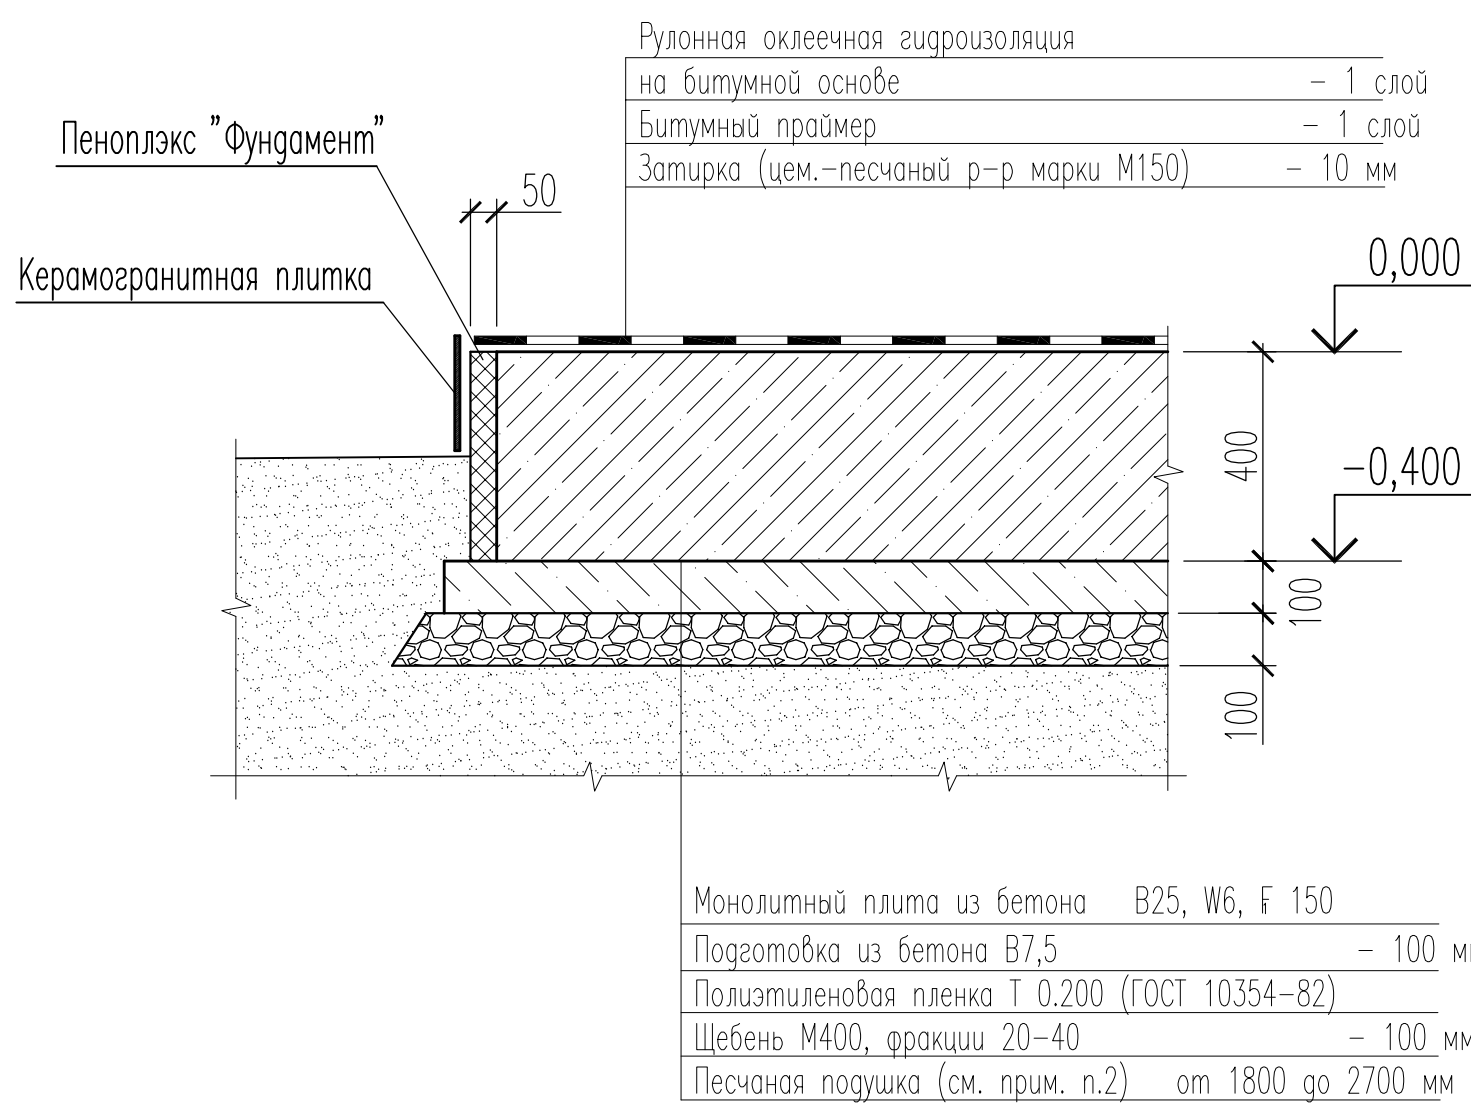

- Данный лист смотреть совместно с листом 2.
- Произвести замену Слоя-1(насыпной слой) и Слоя-2(почвенно-растительный слой) на уплотненную песчаную подушку из песков мелких заглубленную в метериковые грунты ИГЭ-1 (суглинок полутвердый) и ИГЭ-2(песок пылеватый) не менее 200 мм. Уплотнение выполнить послойно (толщина слоя 150-200 мм) до следующих физико-механических характеристик :
 - плотность сухого грунта не менее 1.65 т/м3;
 - угла внутреннего трения не менее 28°;
 - модуль деформации не менее 15 МПа;
 - коэффициент пористости не менее 0,75.
- Под монолитным фундаментом выполнить бетонную подготовку, толщиной 100 мм из бетона В 7,5, размерами на 100 мм в каждую сторону больше размеров подошв фундаментов. Подготовка выполняется по слою щебня втрамбованного в грунт толщиной 100 мм.
- Боковые поверхности конструкций соприкасающиеся с грунтом покрыть двумя слоями битумной мастики по слою битумного праймера.
- Обратную засыпку пазух производить песками мелкими с уплотнением (слоями толщиной 150-200 мм) до плотности сухого грунта не менее 1.65 тс/м3 и коэффициентом уплотнения не менее 0,95.

						8-25-КР			
						Устройство модульного спортивного сооружения по адресу: Самарская область, г.о. Самара, Железнодорожный район, ул. Спортивная, на территории земельных участков с кадастровыми номерами 63:01:0104002:1115, 63:01:0104002:1117			
Изм.	Кол. уч.	Лист	N док.	Подп.	Дата	Конструктивные решения	Стадия	Лист	Листов
Разраб.		Кудашкина		Шваб	06.25		Р	3	
Н.контр.	Шурыгин			Шваб	06.25	Сечения 1-1 - 5-5 к схеме расположения фундаментных плит		ООО "КПС"	
ГИП	Нефедова			Шваб	06.25				

Technical drawing of a reinforced concrete column cross-section. The column is rectangular with a total width of 2400 mm and a total height of 3000 mm. It features a central vertical core with a width of 1250 mm and a height of 2400 mm. The outer shell has a thickness of 950 mm on the left and 450 mm on the right. Reinforcement is shown as circles with diameters of 12 mm and grade A500C, spaced at 200 mm. Section lines are indicated by arrows and the letter 'Б'.

Technical drawing of a reinforced concrete slab (B) showing dimensions and reinforcement details. The drawing includes the following information:

- Dimensions:**
 - Overall width: 2450
 - Overall height: 2900
 - Horizontal segments: 450, 1200, 1300
 - Vertical segment: 100
- Reinforcement Details:**
 - Top reinforcement: $\varnothing 12$ A500C, spacing 200
 - Bottom reinforcement: $\varnothing 12$ A500C, spacing 200
- Labels:**
 - Section line B-B
 - Section line 1-1
 - Section line 5

Technical drawing of a rectangular reinforced concrete slab (A). The drawing shows the slab's dimensions and reinforcement details.

Dimensions:

- Overall width: 1165
- Overall height: 1300
- Top edge offset: 450
- Internal width dimension: 3635

Reinforcement Details:

- Top reinforcement: $\varnothing 12$ A500C, spacing 200.
- Bottom reinforcement: $\varnothing 12$ A500C, spacing 200.

Section Markers:

- Section A-A is indicated by a dashed line across the top.
- Section 1-1 is indicated by a dashed line across the bottom.

Марка, поз.	Обозначение	Наименование	Кол.	Масса ед.кг	Примечание
		Щебень М400, фракции 20-40	3.2		м³
		Бетон В7.5	3		м³
		Бетон В25, W6, F1 200	5.5		м³
		Ø12 А500С ГОСТ 34028-2016 дбш. =	778	0.888	п.м
		Ø10 А240 ГОСТ 34028-2016 дбш. =	66	0.617	п.м

1-1

500

Ø 12 A500C was 200

Ø 12 A500C was 200

с.с.20

с.с.40

Ø 12 A500C was 200

60 200 was 200

с.с.30

с.с.40

200

+0,125
+0,085

-0,075
-0,115

Фиксатор Ф10 А240 was 600x600 в шахм. порядк

						8-25-КР			
						Устройство модульного спортивного сооружения по адресу: Самарская область, г.о. Самара, Железнодорожный район, ул. Спортивная, на территории земельных участков с кадастровыми номерами 63:01:0104002:1115, 63:01:0104002:1117			
Изм.	Кол. уч.	Лист	N док.	Подп.	Дата	Конструктивные решения	Стадия	Лист	Листов
Разраб.		Кудашкина		<i>М.А.З.</i>	06.25		Р	5	
Н.контр.		Шурьгин		<i>Шурьгин</i>	06.25	Схемы армирования фундаментных плит Фп-2, Фп-3 и Фп-4	ООО "КПСР"		
ГИП		Нефедова		<i>Нефедова</i>	06.25				