

Свидетельство о допуске к определенному виду работ, которые оказывают влияние на безопасность объекта капитального строительства № 0073.03-2017-7735116621-П-163 от 11.05.2017

**ПРОВЕДЕНИЕ РАБОТ ПО БЛАГОУСТРОЙСТВУ ТЕРРИТОРИИ
(ЕЕ ЭЛЕМЕНТОВ) ДЛЯ СОЗДАНИЯ «УМНОЙ» СПОРТИВНОЙ ПЛОЩАДКИ
ПО АДРЕСУ:**

**КАДАСТРОВЫЕ НОМЕРА УЧАСТКОВ: 63:01:0104002:1115, 63:01:0104002:1117.
САМАРСКАЯ ОБЛАСТЬ, Г. САМАРА, ЖЕЛЕЗНОДОРОЖНЫЙ РАЙОН, УЛ.
СПОРТИВНАЯ.**

ПРОЕКТНАЯ ДОКУМЕНТАЦИЯ

*Раздел 2. ПЗУ «Схема планировочной
организации земельного участка»*

8-25-ПЗУ

Изм.	№ док.	Подп.	Дата

**Общество с ограниченной ответственностью
«КУЙБЫШЕВСКИЙ ПРОМСТРОЙПРОЕКТ»**

Заказчик: АО «Ситроникс»

**Проведение работ по благоустройству территории
(ее элементов) для создания «умной» спортивной
площадки**

ПРОЕКТНАЯ ДОКУМЕНТАЦИЯ

Раздел 2. Схема планировочной организации земельного участка

8-25-ПЗУ

Том 2

Изм.	№ док.	Подп.	Дата

Инов. № подл.	Подпись и дата	Взам. инв. №

2025

Общество с ограниченной ответственностью
«КУЙБЫШЕВСКИЙ ПРОМСТРОЙПРОЕКТ»

Заказчик: АО «Ситроникс»

Проведение работ по благоустройству территории
(ее элементов) для создания «умной» спортивной
площадки

ПРОЕКТНАЯ ДОКУМЕНТАЦИЯ

Раздел 2. Схема планировочной организации земельного участка

8-25-ПЗУ

Том 2

Изм.	№ док.	Подп.	Дата

Главный инженер

Главный инженер проекта



Е.Б.Шурыгин

О. А. Нефедова



2025

Взам. инв. №	
Подпись и дата	
Инв. № подл.	

Содержание:

№	Название раздела	Лист
	Содержание	
а	характеристика земельного участка, представленного для размещения объекта капитального строительства	2
а ₁	сведения о наличии зон с особыми условиями использования территории в пределах границ земельного участка	3
б	обоснование границ санитарно-защитных зон объектов капитального строительства в пределах границ земельного участка	3
в	обоснование и описание планировочной организации земельного участка в соответствии с градостроительным и техническими регламентами либо документами об использовании земельного участка	4
г	технико-экономические показатели земельного участка, предоставленного для размещения объекта капитального строительства	5
д	обоснование и описание решений по инженерной подготовке территорий, в том числе решений по инженерной защите территории и объектов капитального строительства от последствий опасных геологических процессов, паводковых, поверхностных и грунтовых вод	5
е	описание организации рельефа вертикальной планировкой	5
ж	описание решений по благоустройству территории	6
л	обоснование схем транспортных коммуникаций, обеспечивающих внешний и внутренний подъезд к объекту капитального строительства	6
	Ссылочные и прилагаемые документы:	
	Постановление о выдаче разрешения на право вырубki зеленых насаждений № 119 от 17.04.2025 выдано администрацией Железнодорожного внутригородского района городского округа Самара	
	Графическая часть:	
	Ситуационный план	Лист 1
	Схема планировочной организации земельного участка М 1:500	Лист 2
	План организации рельефа М 1:500	Лист 3
	План земляных масс М 1:500	Лист 4
	Узлы и детали проездов, тротуаров	Лист 5

					00-ПЗУ		
Изм.	Лист	№ докум.	Подпись	Дата			
ГИП		Нефедова			Устройство модульного спортивного сооружения по адресу: Самарская область, г.о.Самара, Железнодорожный район, ул.Спортивная, на территории ЗУ с КН 63:01:0104002:1115, КН 63:01:0104002:1117		
Разраб.		Нерода					
Проверил		Нефедова			Стадия Лист Листов П 1 Общество с ограниченной ответственностью «Самарский Промстройпроект»		

Раздел 2 «Схема планировочной организации земельного участка».

а) характеристика земельного участка, представленного для размещения объекта капитального строительства

Земельный участок, предоставленный под устройство модульного спортивного сооружения расположен по адресу: Самарская область, г.о. Самара, Железнодорожный район, ул. Спортивная, на территории земельных участков с кадастровыми номерами 63:01:0104002:1115, 63:01:0104002:1117.

В границах земельных участков расположены объекты капитального строительства: с кадастровым номером 63:01:0104002:1115 — 2 единицы, с кадастровым номером 3:01:0104002:1117 — 1 единица.

Рельеф равнинный, с уклоном на юг. Максимальная абсолютная отметка 72.18м, минимальная абсолютная отметка 69.25м.

Древесно-кустарниковая растительность представлена отдельно стоящими деревьями. (Постановление о выдаче разрешения на право вырубki зеленых насаждений № 119 от 17.04.2025 выдано администрацией Железнодорожного внутригородского района городского округа Самара).

Земельные участки с кадастровыми номерами 63:01:0104002:1115, 63:01:0104002:1117 под устройство модульного спортивного сооружения расположены на территории детского парка культуры и отдыха им. Щорса (южная сторона парка).

С восточной стороны от рассматриваемого участка расположена территория существующего детского сада.

Существующие сети связи и электроснабжения подлежат выносу до начала строительства.

По земельным участкам с кадастровыми номерами 63:01:0104002:1115, 63:01:0104002:1117 проходят ограничения и обременения в части охранных зон коммуникаций.

Площадь земельного участка с КН 63:01:0104002:1117 — 2128м².

Площадь земельного участка с КН 63:01:0104002:1115 — 2299м².

а1) сведения о наличии зон с особыми условиями использования территории в пределах границ земельного участка

Кадастровый номер земельного участка 63:01:0104002:1115.

Отведенный участок проектирования частично или полностью расположен в границах зон с особыми условиями использования территории:

ЧЗУ: 1115/1 «вид ограничения (обременения): прочие ограничения прав и обременения объекта недвижимости; Срок действия: не установлен; Содержание ограничения (обременения): Часть участка находится в охрannой зоне коммуникаций» Земельный участок (земельные участки) частично расположен (расположены) в границах зоны с особыми условиями использования территории, площадь земельного участка (земельных участков), покрываемая зоной с особыми условиями территории, составляет «224» м²;

						00-ПЗУ	Лист 2
Изм.	Кол.уч.	Лист	№ док.	Подп.	Дата		

ЧЗУ: 1115/2 «вид ограничения (обременения): ограничения прав на земельный участок, предусмотренные статьей 56 Земельного кодекса Российской Федерации; Срок действия: не установлен; реквизиты документа-основания: постановление Правительства Самарской области от 11.12.2014 № 775 выдан: Правительство Самарской области; Содержание ограничения (обременения): Утверждены Постановлением Правительства Самарской области от 11.12.2014 № 775 «О внесении изменений в постановление Правительства Самарской области от 05.05.2012 № 243 «Об утверждении границ зон охраны объектов культурного наследия федерального значения, расположенных на территории Самарской области, режимов использования земель и градостроительных регламентов в границах данных зон»; Реестровый номер границы: 63.01.2.409» Земельный участок (земельные участки) частично расположен (расположены) в границах зоны с особыми условиями использования территории, площадь земельного участка (земельных участков), покрываемая зоной с особыми условиями территории, составляет «485» м²;

ЧЗУ: 1115/3 «вид ограничения (обременения): ограничения прав на земельный участок, предусмотренные статьей 56 Земельного кодекса Российской Федерации; Срок действия: не установлен; Земельный участок (земельные участки) частично расположен (расположены) в границах зоны с особыми условиями использования территории, площадь земельного участка (земельных участков), покрываемая зоной с особыми условиями территории, составляет «255» м²;

- «вид ограничения (обременения): ограничения прав на земельный участок, предусмотренные статьей 56 Земельного кодекса Российской Федерации; Срок действия: не установлен; реквизиты документа-основания: об установлении приаэродромной территории аэродрома экспериментальной авиации Самара (Безымянка), покрываемая зоной с особыми условиями территории, составляет «2299» м²;

- «Приаэродромная территория, Наименование охраняемого объекта: Аэродром экспериментальной авиации Самара Вид зоны (наименование) по документу: Подзона 4;

- «Приаэродромная территория, Наименование охраняемого объекта: Аэродром экспериментальной авиации Самара Вид зоны (наименование) по документу: Подзона 5;

- «Приаэродромная территория, Наименование охраняемого объекта: Аэродром экспериментальной авиации Самара Вид зоны (наименование) по документу: Подзона 6.

Покрываемая зоной с особыми условиями территории, составляет «2299» м²;

- «Приаэродромная территория Наименование охраняемого объекта: Аэродром экспериментальной авиации Самара Вид зоны (наименование) по документу: Подзона 3 Сектор 48 Ограничения: Н=190,72м». Земельный участок (земельные участки) полностью расположен (расположены) в границах зоны с особыми условиями использования территории, площадь земельного участка (земельных участков), покрываемая зоной с особыми условиями территории, составляет «2299» м².

Кадастровый номер земельного участка 63:01:0104002:1117.

Отведенный участок проектирования частично или полностью расположен в границах зон с особыми условиями использования территории:

ЧЗУ: 1117/1 «вид ограничения (обременения): прочие ограничения прав и обременения объекта недвижимости; Срок действия: не установлен; Содержание ограничения (обременения): Часть участка находится в охранной зоне коммуникаций» Земельный участок (земельные участки) частично расположен (расположены) в границах зоны с особыми условиями использования территории, площадь земельного участка (земельных участков), покрываемая зоной с особыми условиями территории, составляет «121» м²;

						00-ПЗУ	Лист 3
Изм.	Кол.уч.	Лист	№ док.	Подп.	Дата		

- «вид ограничения (обременения): ограничения прав на земельный участок, предусмотренные статьей 56 Земельного кодекса Российской Федерации; Срок действия: не установлен; Земельный участок полностью расположен в границах зоны с особыми условиями использования территории, площадь земельного участка (земельных участков), покрываемая зоной с особыми условиями территории, составляет «2128» м²;
- «вид ограничения (обременения): ограничения прав на земельный участок, предусмотренные статьей 56 Земельного кодекса Российской Федерации; Срок действия: не установлен; реквизиты документа-основания: об установлении приаэродромной территории аэродрома экспериментальной авиации Самара (Безымянка), покрываемая зоной с особыми условиями территории, составляет «2128» м²;
- «Приаэродромная территория, Наименование охраняемого объекта: Аэродром экспериментальной авиации Самара Вид зоны (наименование) по документу: Подзона 4;
- «Приаэродромная территория, Наименование охраняемого объекта: Аэродром экспериментальной авиации Самара Вид зоны (наименование) по документу: Подзона 5;

б) обоснование границ санитарно-защитных зон объектов капитального строительства в пределах границ земельного участка

Участки под устройство модульного спортивного сооружения не попадает в утвержденные границы ЗСО подземных и поверхностных питьевых водозаборов.

в) обоснование и описание планировочной организации земельного участка в соответствии с градостроительным и техническим регламентами либо документами об использовании земельного участка

Основанием для разработки схемы планировочной организации земельного участка под строительство многоквартирного жилого дома послужили следующие материалы:

1. Градостроительные планы земельных участков: № РФ-63-3-01-0-00-2025-0239-0 от 14.04.2025г., № РФ-63-3-01-0-00-2025-0224-0 от 11.04.2025г.
2. Задание на выполнение проектных работ;
3. Материалы топографической съемки;
7. Технические задания и архитектурно-строительные решения.

Кадастровый номер земельного участка 63:01:0104002:1115. Земельный участок расположен в территориальной зоне Ц-4с, установлен градостроительный регламент. Объект относится к основному виду разрешенного использования земельного участка: площадки для занятия спортом — (5.1.3).

Установлен градостроительный регламент, пункт 2.1 ГПЗУ № РФ-63-3-01-0-00-2025-0239-0 — Дума городского округа Самара, Постановление Самарской Городской Думы от 26.04.2001 года № 61.

Объекты, включенные в единый государственный реестр объектов культурного наследия (памятников истории и культуры) – информация отсутствует.

Постановление Администрации г.о. Самара от 17.12.2019 № 977 «Об утверждении документации по планировке территории (проекта межевания территорий, занимаемых многоквартирными жилыми домами в границах улиц Спортивная, Чернореченская, Желябова, Урицкого, Красноармейская в городском округе Самара) в Железнодорожном и Ленинском районах городского округа Самара», Постановление Администрации г.о. Самара от 17.10.2022 № 863 «Об утверждении документации по планировке территории (проект

						00-ПЗУ	Лист 4
Изм.	Кол.уч.	Лист	№ док.	Подп.	Дата		

межевания территории) по внесению изменений в документацию по планировке территории (проект межевания территорий, занимаемых многоквартирными жилыми домами в границах улиц Спортивная, Чернореченская, Желябова, Урицкого, Красноармейская в городском округе Самара) в Железнодорожном и Ленинском районах городского округа Самара, утвержденную постановлением Администрации городского округа Самара от 17.12.2019 № 977 «Об утверждении документации по планировке территории (проекта межевания территорий, занимаемых многоквартирными жилыми домами в границах улиц Спортивная, Чернореченская, Желябова, Урицкого, Красноармейская в городском округе Самара) в Железнодорожном и Ленинском районах городского округа Самара»».

Кадастровый номер земельного участка 63:01:0104002:1117. Земельный участок расположен в территориальной зоне Ц-4с, установлен градостроительный регламент. Объект относится к основному виду разрешенного использования земельного участка: площадки для занятия спортом — (5.1.3).

Установлен градостроительный регламент, пункт 2.1 ГПЗУ № РФ-63-3-01-0-00-2025-0239-0 — Дума городского округа Самара, Постановление Самарской Городской Думы от 26.04.2001 года № 61.

Объекты, включенные в единый государственный реестр объектов культурного наследия (памятников истории и культуры) – информация отсутствует.

Постановление Администрации г.о. Самара от 17.12.2019 № 977 «Об утверждении документации по планировке территории (проекта межевания территорий, занимаемых многоквартирными жилыми домами в границах улиц Спортивная, Чернореченская, Желябова, Урицкого, Красноармейская в городском округе Самара) в Железнодорожном и Ленинском районах городского округа Самара», Постановление Администрации г.о. Самара от 17.10.2022 № 863 «Об утверждении документации по планировке территории (проект межевания территории) по внесению изменений в документацию по планировке территории (проект межевания территорий, занимаемых многоквартирными жилыми домами в границах улиц Спортивная, Чернореченская, Желябова, Урицкого, Красноармейская в городском округе Самара) в Железнодорожном и Ленинском районах городского округа Самара, утвержденную постановлением Администрации городского округа Самара от 17.12.2019 № 977 «Об утверждении документации по планировке территории (проекта межевания территорий, занимаемых многоквартирными жилыми домами в границах улиц Спортивная, Чернореченская, Желябова, Урицкого, Красноармейская в городском округе Самара) в Железнодорожном и Ленинском районах городского округа Самара»».

Планировочное решение организации земельного участка увязано с существующим благоустройством, здание и сооружения размещены на нормативных расстояниях друг от друга.

Планируемое использование земельного участка – устройство модульного спортивного сооружения, расположенного по адресу: Самарская область, г.о. Самара, Железнодорожный район, ул. Спортивная, на территории земельных участков с кадастровыми номерами 63:01:0104002:1115, 63:01:0104002:1117.

На проектируемой территории предусмотрено размещение следующих зданий и сооружений:

- проектируемое административно-бытовое сооружение «Фиджитал центр» (№1 по табл. «Экспликация зданий и сооружений»);
- зона воркаута и тренажеров (№2 по табл. «Экспликация зданий и сооружений»);
- зона баскетбола 3х3 (№3 по табл. «Экспликация зданий и сооружений»);

						00-ПЗУ	Лист 5
Изм.	Кол.уч.	Лист	№ док.	Подп.	Дата		

- зона для мини-футбола (№4 по табл. «Экспликация зданий и сооружений»);
- зона общественного питания (№5 по табл. «Экспликация зданий и сооружений»);
- стоянка для машин (№6 по табл. «Экспликация зданий и сооружений»);
- велопарковка (№7 по табл. «Экспликация зданий и сооружений»);
- площадка для ТБО (№8 по табл. «Экспликация зданий и сооружений»).

г) технико-экономические показатели земельного участка, предоставленного для размещения объекта капитального строительства

Технико-экономические показатели земельного участка представлены в таблице 1.
Технико-экономические показатели

Таблица 1

№	Наименование	Количество	%
1	Площадь участка по ГПЗУ №РФ-63-3-01-0-00-2025-0239-0 № РФ-63-3-01-0-00-2025-0224-0	2128,0 м ² 2299,0м ² 4427,0м ²	
2	Площадь участка в границах благоустройства	4463,74 м ²	100
3	Площадь застройки	464,50 м ²	10,4
3	Площадь твердых покрытий в границах благоустройства	2951,7м ²	66,0
4	Площадь озеленения в границах благоустройства	1047,5 м ²	23,6
5	Коэффициент застройки		10

д) обоснование и описание решений по инженерной подготовке территорий, в том числе решений по инженерной защите территории и объектов капитального строительства от последствий опасных геологических процессов, паводковых, поверхностных и грунтовых вод

Схема инженерной подготовки территории разработана в соответствии с архитектурно-планировочным и технологическим решениями застройки.

В целях обеспечения уровня благоустройства предусматриваются следующие мероприятия по инженерной подготовке территории: вертикальная планировка и организация рассредоточенного стока поверхностных вод по лоткам проездов в проектируемые дождеприемники Дп-1, Дп-2.

е) описание организации рельефа вертикальной планировкой

Выбор планировочных отметок участка определен с учетом отметок существующей, прилегающей, благоустроенной территории. Проектом принята сплошная система вертикальной планировки. Проект организации рельефа выполнен методом проектных (красных) горизонталей с шагом 0,10м и решена в балансе насыпи и выемке участка.

Схема водоотвода с территории запроектирована с таким расчетом, чтобы всю поверхностную воду отвести от проектируемого объекта с выпуском воды в проектируемые дождеприемные колодцы (ДП-1,2).

						00-ПЗУ	Лист 6
Изм.	Кол.уч.	Лист	№ док.	Подп.	Дата		

В связи с перепадом высот существующего благоустройства и проектируемого рельефа, организация рельефа выполнена с устройством проектируемых откосов по всему периметру участка.

Отметка здания, принятая за отм. 0,000 равна 71.70м.

Продольные и поперечные уклоны по проездам и тротуарам приняты в пределах допусков, предусмотренных нормами, и находятся в диапазоне от 6‰ до 22‰, уклоны на путях движения МГН находятся в диапазоне от 5‰ до 62‰.

Проектные отметки здания и рельефа назначены с учетом существующего уклона территории, организации водоотвода и в увязке с существующей территорией. Водоотвод с тротуаров производится по поперечному уклону на проектируемую проезжую часть.

ж) описание решений по благоустройству территории

В проекте приняты следующие решения по благоустройству территории:

- устройство подъездов и тротуаров на спортивного сооружения с покрытием из брусчатки;
- предусмотрена возможность подъезда пожарных машин на расстоянии 6.0м от главного фасада сооружения;
- устройство отмотки;
- устройства площадки паркования а/машин на 5 м/м , включая 1м/м для МГН;
- устройство велопарковки на 10 мест;
- устройства площадки для установки мусоросборников;
- установка урн и скамеек;
- устройство озеленения на свободных от застройки и покрытий участках;
- укрепление откосов насыпи посевом трав по растительному грунту.

Спортивный объект имеет ограждение по всему периметру. Проезды запроектированы шириной 8,50м с асфальтобетонным покрытием и бордюром типа БР100.30.15 по ГОСТ 6665-91. Радиусы закругления приняты 5.0 и 6.0м. Тротуары и отмотки предусмотрены в покрытии плиткой бетонной тротуарной с бордюром из бортового камня типа БР100.20.8 по ГОСТ 6665-91. На прилегающей к территории спортивного сооружения (существующий проезд) проектом предусмотрен ремонт дорожной одежды.

Для создания газонов используется растительный грунт. Для их устройства применяется смесь трав, наиболее устойчивая к вытаптыванию: овсяница красная, мятлик луговой, рейграс пастбищный.

л) обоснование схем транспортных коммуникаций, обеспечивающих внешний и внутренний подъезд к объекту капитального строительства, - для объектов непроизводственного назначения

Схема транспортных коммуникаций, обеспечивающих подъезд к проектируемому объекту выполнена по средствам организации примыкания проектируемого проезда к существующему местному проезду.

						00-ПЗУ	Лист 7
Изм.	Кол.уч.	Лист	№ док.	Подп.	Дата		

Ссылочные и прилагаемые документы


При разработке данной проектной документации были использованы нормативные и технические документы:

Таблица 2

Обозначение	Наименование	Примечание
	<u>Ссылочные документы</u>	
Федеральный закон №123-ФЗ	Технический регламент о требованиях пожарной безопасности	
СП 42.13330.2016 Актуализированная редакция СНиП 2.07.01-89* (с Изменениями N 1, 2, 3, 4)	Градостроительство. Планировка и застройка городских и сельских поселений.	
СП 34.13330.2021 «СНиП 2.05.02-85* Автомобильные дороги»	Автомобильные дороги	
СП 59.13330.2020 Актуализированная редакция	Доступность зданий и сооружений для маломобильных групп населения СНиП 35-01-2001	
СП 332.1325800.2017	Спортивные сооружения. Правила проектирования	
СП 2.1.3678-20	«Санитарно-эпидемиологические требования к эксплуатации помещений, зданий, сооружений, оборудования и транспорта, а также условиям деятельности хозяйствующих субъектов, осуществляющих продажу товаров, выполнение работ или оказание услуг»	

Согласовано:


	Взам. инб.	№
	Подп. и дата	
Инб. подл.		

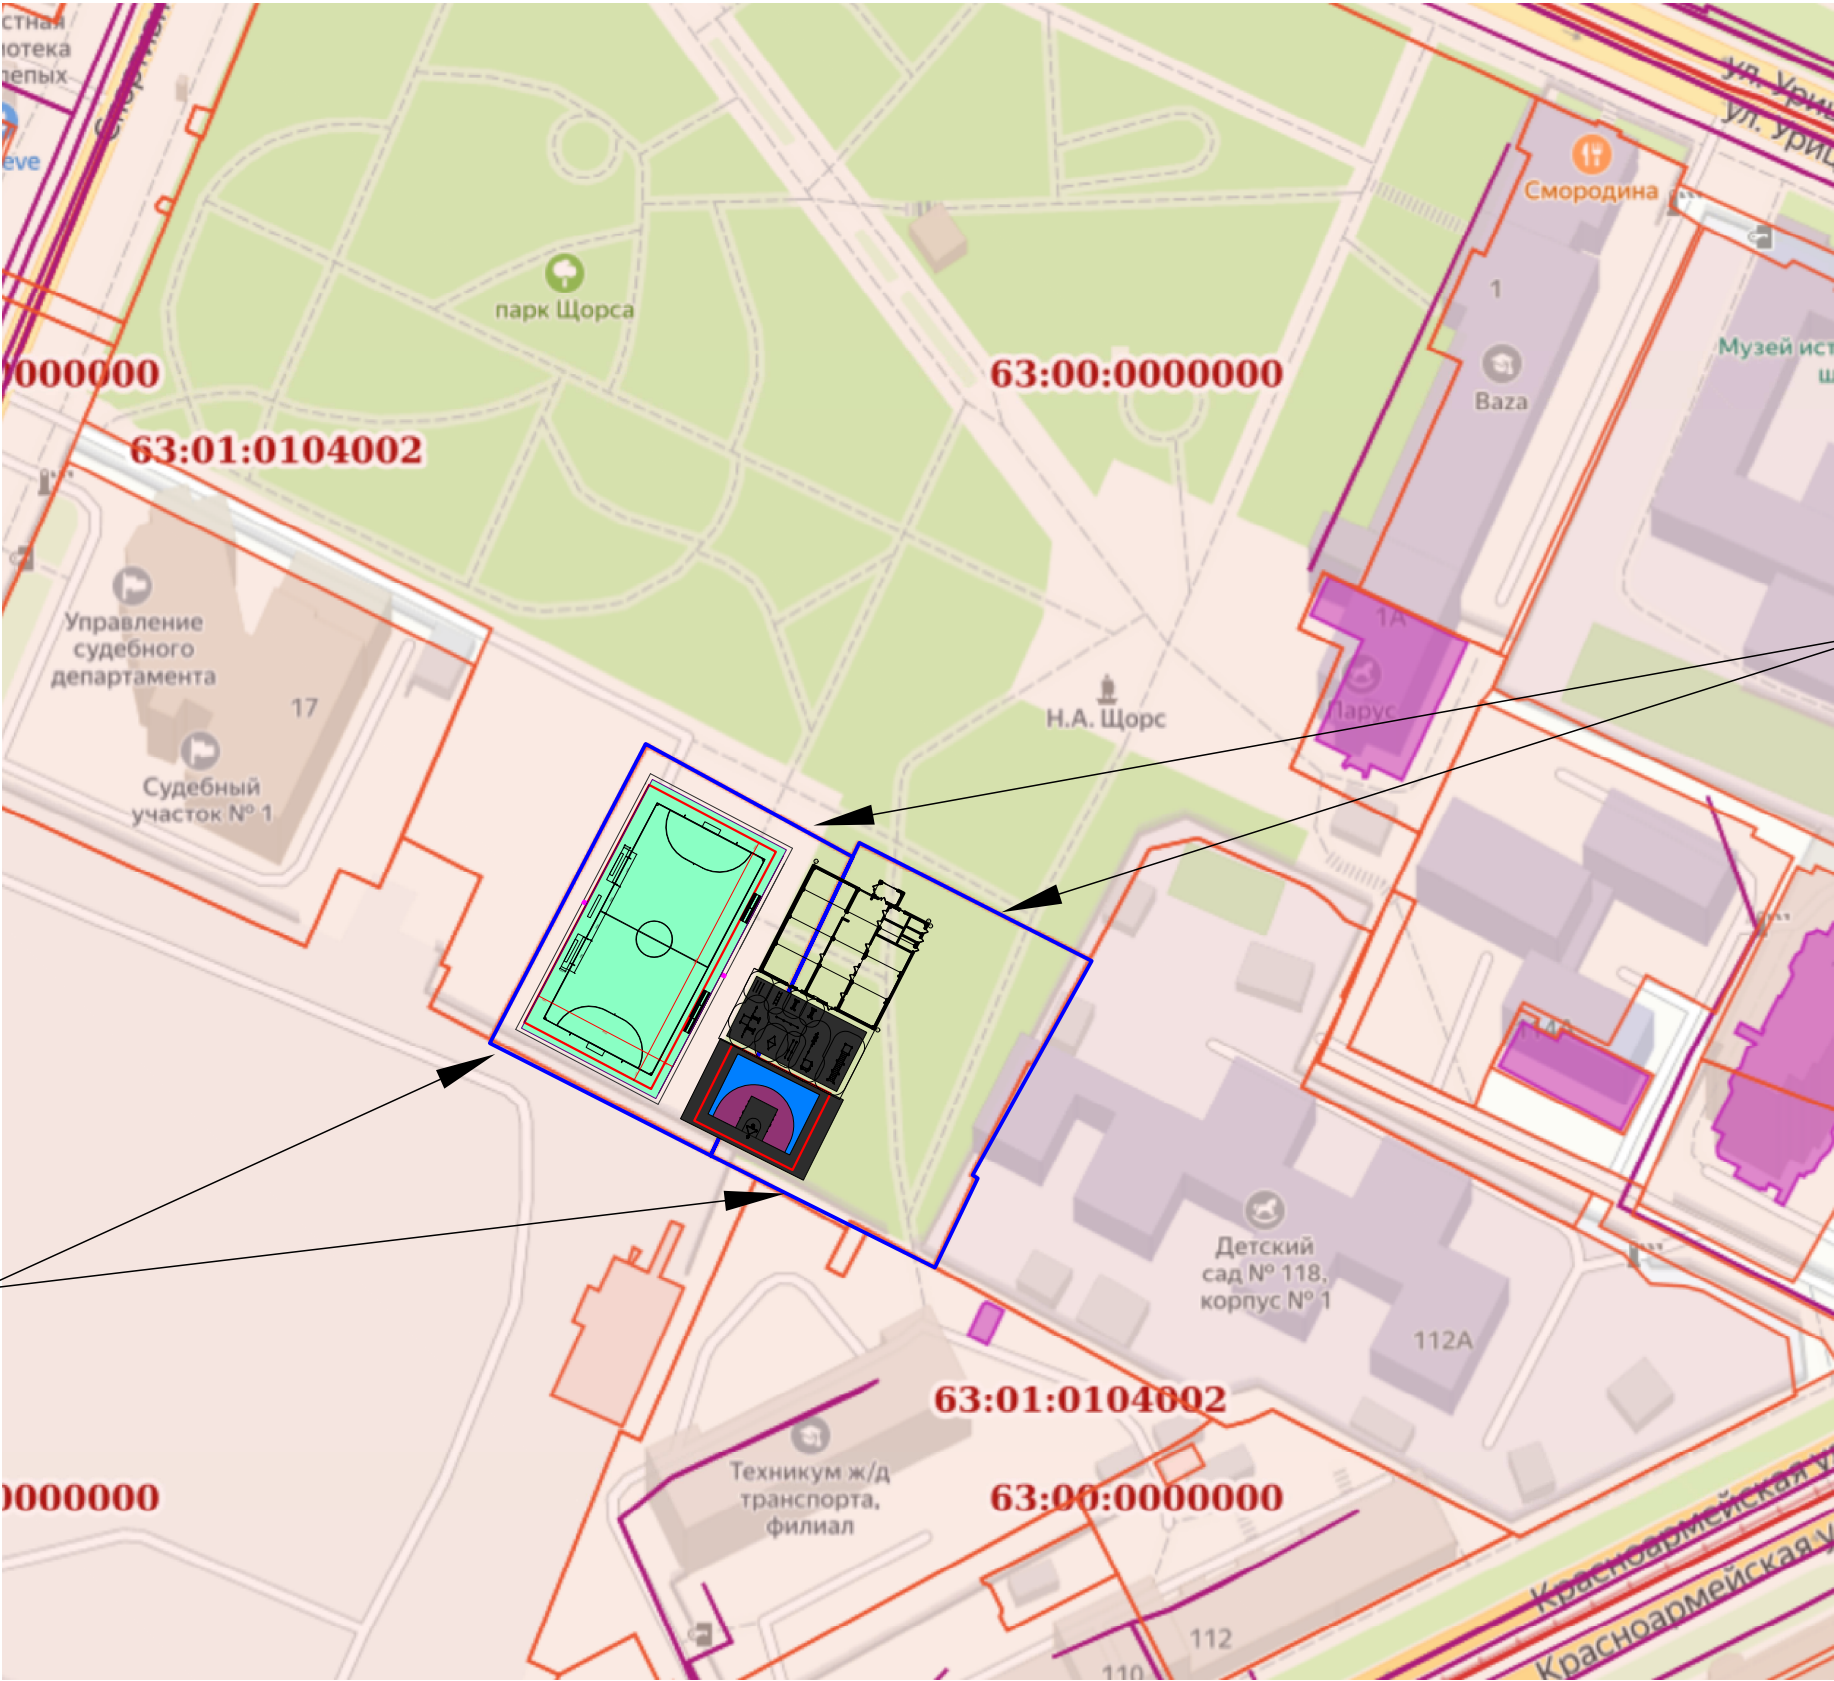

Кадастровые номера участков
63:01:0104002:1115,
63:01:0104002:1117

Проектируемые участки

						00-ПЗУ			
						Устройство модульного спортивного сооружения по адресу: Самарская область, г.о. Самара, Железнодорожный район, ул. Спортивная, на территории земельных участков с кадастровыми номерами 63:01:0104002:1115, 63:01:0104002:1117			
Изм.	Кол.уч	Лист	N док	Подпись	Дата	Схема планировочной организации земельного участка	Стадия	Лист	Листов
Разраб.		Нерода			04.2025		П	1	
Н.контр.		Шурыгин				Ситуационный план М 1:5000	Общество с ограниченной ответственностью "Самарский Промстройпроект"		
ГИП		Нефедова							

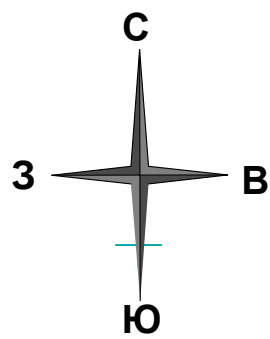

ВЕДОМОСТЬ МАЛЫХ ФОРМ АРХИТЕКТУРЫ


Поз.	Обозначение	Артикул, наименование	Кол.	Примечание
1		Скамья со спинкой ДХО 06190	2	TORUDA комфортная среда info@toruda-park.ru
2		Арт. Н123884 Урна уличная TORUDA 25	1	
3		Арт. ДХО 04010 Велопарковка на 10 мест	1	
4		Мусорные контейнеры на 600л	6	
5		Арт. Н129626 Навес для мусорных на шесть контейнеров 6000x2000x2250 мм	1	

ЭКСПЛИКАЦИЯ ЗДАНИЙ И СООРУЖЕНИЙ

№ п.п.	Наименование	Площадь застройки, м2
1	Административно-бытовое сооружение "Фиджитал центр"	464.50
2	Зона воркаута и тренажеров (22,5м x12,0м)	270,0
3	Зона баскетбола 3х3(стритбола)	330,75
4	Зона для мини-футбола 40мx20м	1251,60
5	Зона общественного питания	
6	Стоянка для машин в т. ч. для МГН	
7	Велопарковка на 10 мест	
8	Площадка для ТБО (6 конт.)	

УСЛОВНЫЕ ОБОЗНАЧЕНИЯ

	Ремонт а/б покрытия проезжей части (дет. тип 1)
	Проектируемое покрытие отмотки (дет. тип 2)
	Проектируемое покрытие тротуара (дет. тип 3)
	Проектируемое покрытие футбольного поля (дет. тип 4)
	Проектируемое покрытие игровой площадки баскетбол (дет. тип 5)
	Обременение участка 63:01:0104002:1115/1
	Обременение участка (охранная зона объектов культурного наследия федерального значения) 63:01:0104002:1115/2
	Обременение участка (охранная зона сетей) 63:01:0104002:1115/3
	Обременение участка (охранная зона сетей, охранная зона объектов культурного наследия федерального значения) 63:01:0104002:1117/1
	Граница земельного участка 63:01:0104002:1115
	Граница земельного участка 63:01:0104002:1117
	Граница благоустройства территории
	Проектируемое устройство газонов
	Проектируемое ограждение спортивных площадок
	Покрытие буферной зоны вокруг футбольного поля (дет. тип 7)
	Проектируемое а/б покрытие проезжей части (дет. тип 6)
	Установка тротуарного борта БР 100x20x8
	Установка дорожного борта БР 100x30x15
	Схема движения пожарных машин
	Поворотные точки углов проектируемого здания
	Демонтаж сущ. ограждения

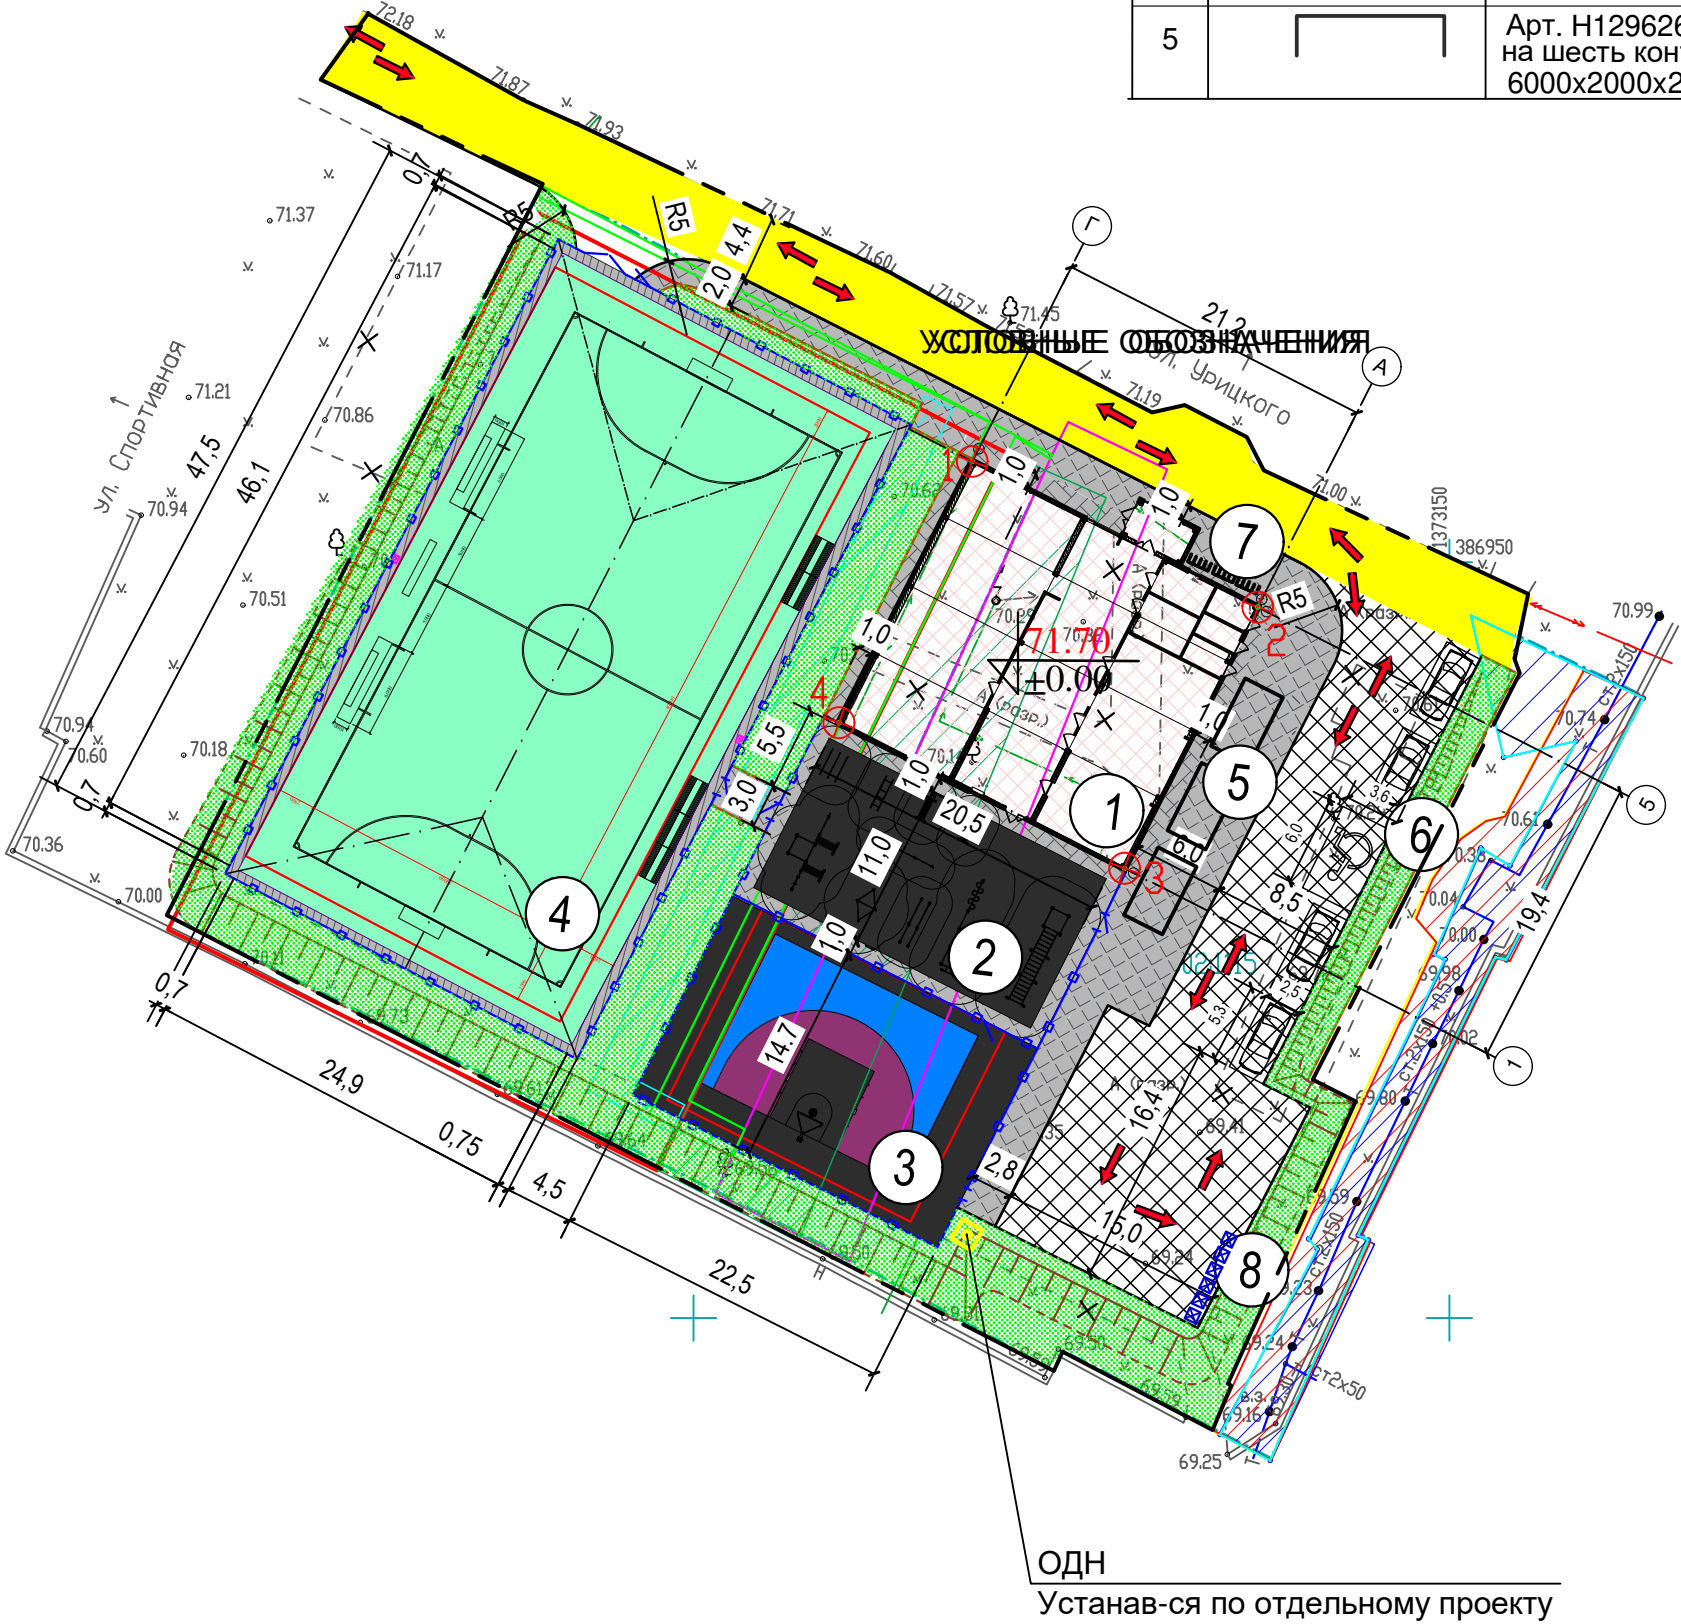

Примечания:

- Некапитальное модульное административно-бытовое сооружение устанавливается на заранее подготовленное основание, в место исключяющее подтопление водой. Допускается максимальный перепад высотных отметок по всей плоскости основания, который не должен превышать 10 мм.
- Система высот Балтийская.
- Система координат - МСК-63
- Все размеры даны в метрах.
- Поворотные точки углов модульного здания №1 даны по разбивочным осям.
- Для защиты откосов от оползания поверхность укрепляется георешеткой объемной из полиэтиленовых лент высотой 150мм с перфорацией с ячейкой 210x210 с заполнением ячеек растительным грунтом с посевом трав тройной нормой высева. Состав травосмесей:- овсяница луговая-35%, овсяница красная-35%, клевер красный (белый) 30%.
- Количество анкеров (анкера забивные из арматурной стали А-I, Ø12мм, длина-900мм) для крепления георешетки - 5шт./м².
- Проектная документация выполнена на основании:
ГПЗУ № РФ-63-3-01-0-00-2025-0239-0, кадастровый номер ЗУ 63:01:0104002:1117;
ГПЗУ № РФ-63-3-01-0-00-2025-0224-0, кадастровый номер ЗУ 63:01:0104002:1115.

ПРОЕКТИРУЕМОЕ ЗДАНИЕ
"Фиджитал центр"

Назв. точки	Координаты	
	х	у
1	1373118.43	386956.65
2	1373137.32	386947.02
3	1373128.50	386929.74
4	1373109.62	386939.37

Согласовано:

Взам. инв. №

Подп. и дата

Инф. лодп.

00-ПЗУ

Устройство модульного спортивного сооружения по адресу:
Самарская область, г.о. Самара, Железнодорожный район, ул. Спортивная,
на территории земельных участков с кадастровыми номерами
63:01:0104002:1115, 63:01:0104002:1117

Разраб.	Нерода		04.2025	Схема планировочной организации земельного участка	Стадия	Лист	Листов
					П	2	
Н.контр.	Шурыгин			Схема планировочной организации земельного участка М 1:500	Общество с ограниченной ответственностью "Самарский Промстройпроект"		
ГИП	Нефедова						



A horizontal number line with 10 equally spaced tick marks. Below each tick mark is a dashed rectangular box for labeling. The boxes are currently empty.

Проектируемый откос

Согласовано:

Инв. подл.

План организации рельефа М 1:500	Общество с ограниченной ответственностью "Самарский Промстройпроект"
-------------------------------------	---

Формат А3

ВЕДОМОСТЬ ОБЪЕМОВ ЗЕМЛЯНЫХ РАБОТ

Наименование грунта	Количество,м³	
	Насыпь	Выемка
	(+)	(-)
1. Грунт планировки территории	4653	—
2. Вытесненный грунт в т.ч. при устройстве:		1538
а) подземных частей зданий (сооружений)	см.раздел смет	
б) автодорожных покрытий		(1231)
в) подземных сетей		(96)
г) плодородной почвы на участках озеленения		(211)
3. Грунт для устройства высоких полов зданий и обвалований сооружений	—	—
4. Поправка на уплотнение 10%	465	—
Всего пригодного грунта	5118	1538
5. Недостаток пригодного грунта		3580
6. Грунт непригодный для устройства насыпи оснований зданий, подлежащих удалению с территории	446***	446***
7. Плодородный грунт. Всего:		
в т.ч. а) используемый для озеленения территории	211	
б) недостаток		211
8. Итого перерабатываемого грунта	5775	5775

*** В отвале

Условные обозначения


Рабочая отметка	+1.54	71.50	Планировочная отметка земли
		69.96	
			Существующая отметка земли

ПРИМЕЧАНИЯ:


1. Картограмма земляных работ выполнена в соответствии с планом организации рельефа участка.
2. В местах подсыпки грунт укладывается слоями толщиной 10-12 см, каждый слой подсыпки хорошо утрамбовывается и поливается водой.
3. Сетка, разбитая на картограмме, не является строительной и служит для подсчета объемов земляных масс. Размерная сетка квадратов привязана границам ЗУ 63:01:0104002:1115.
4. Черные отметки земли в углах сетки квадратов получены путем интерполяции между отметками топографической съемки.

						00-ПЗУ			
						Устройство модульного спортивного сооружения по адресу: Самарская область, г.о. Самара, Железнодорожный район, ул. Спортивная, на территории земельных участков с кадастровыми номерами 63:01:0104002:1115, 63:01:0104002:1117			
Изм.	Кол.уч	Лист	N док	Подпись	Дата	Схема планировочной организации земельного участка	Стадия	Лист	Листов
Разраб.		Нерода			04.2025		П	4	
Н.контр.		Шурыгин				План земляных масс М 1:500	Общество с ограниченной ответственностью "Самарский Промстройпроект"		
ГИП		Нефедова							


тип 1 Ремонт а/б покрытия проезжей части

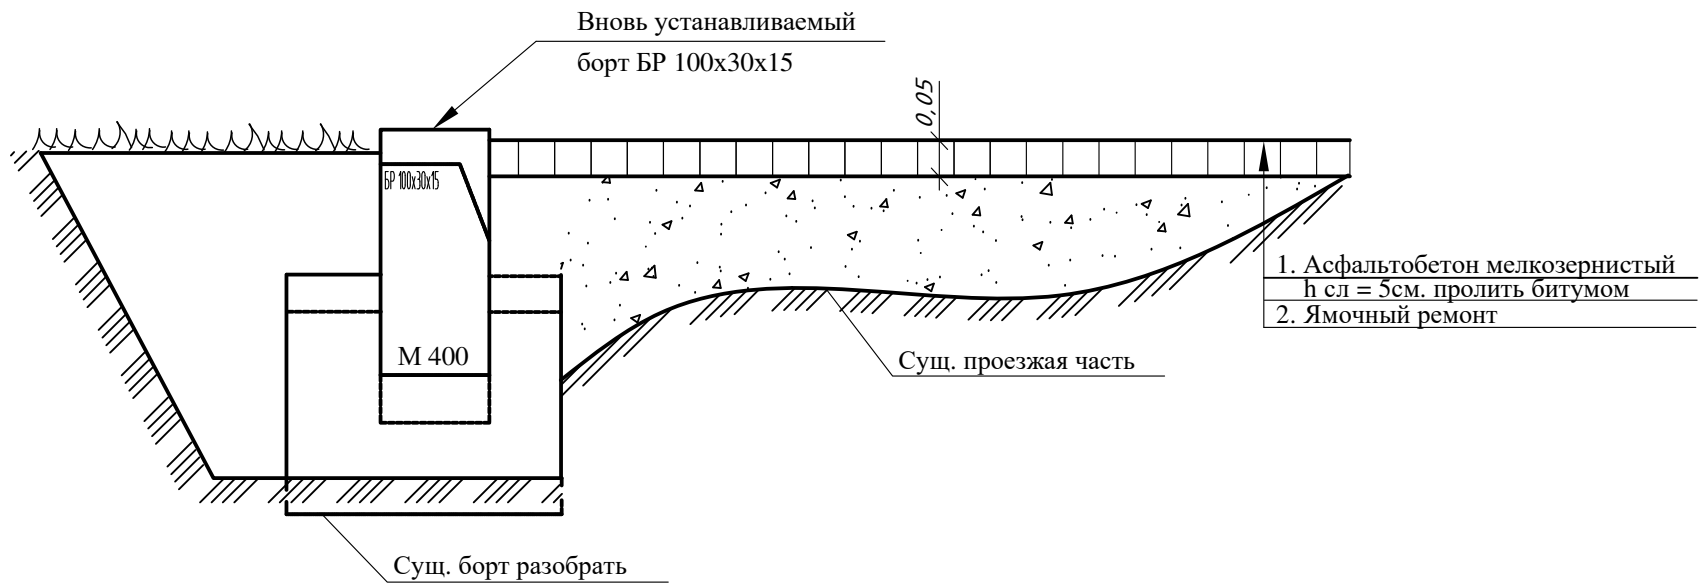


тип 2 Покрытие откоски

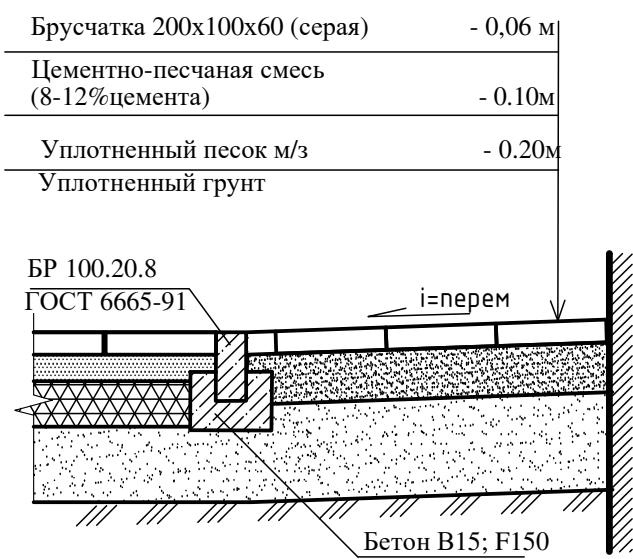


тип 3 Покрытие тротуара

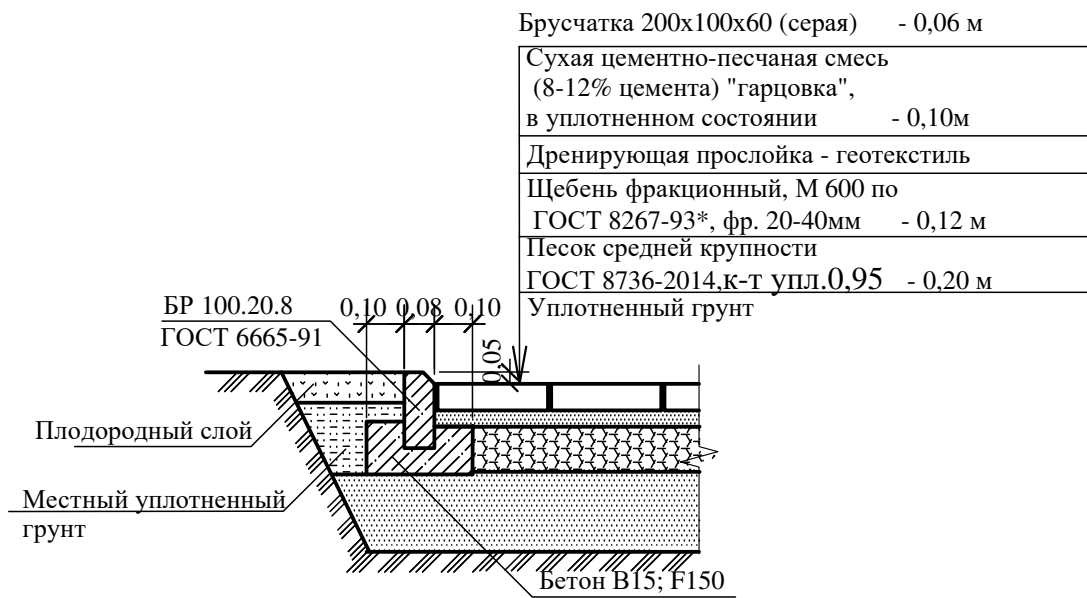


тип 4 Покрытие футбольного поля

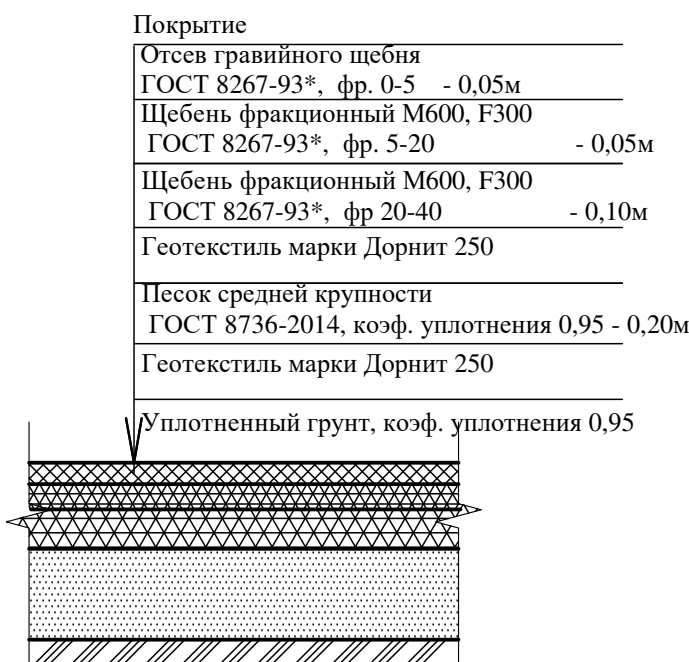

тип 5 Покрытие игровой площадки баскетбол

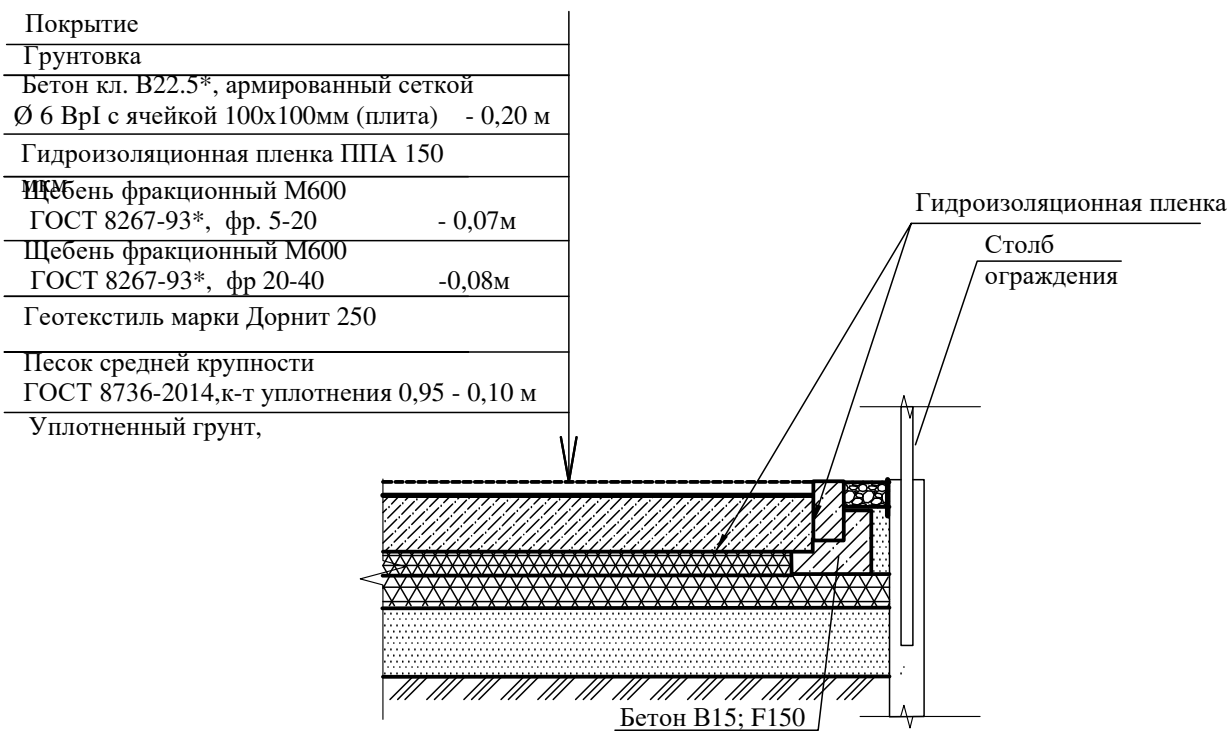


тип 6 Покрытие проезжей части

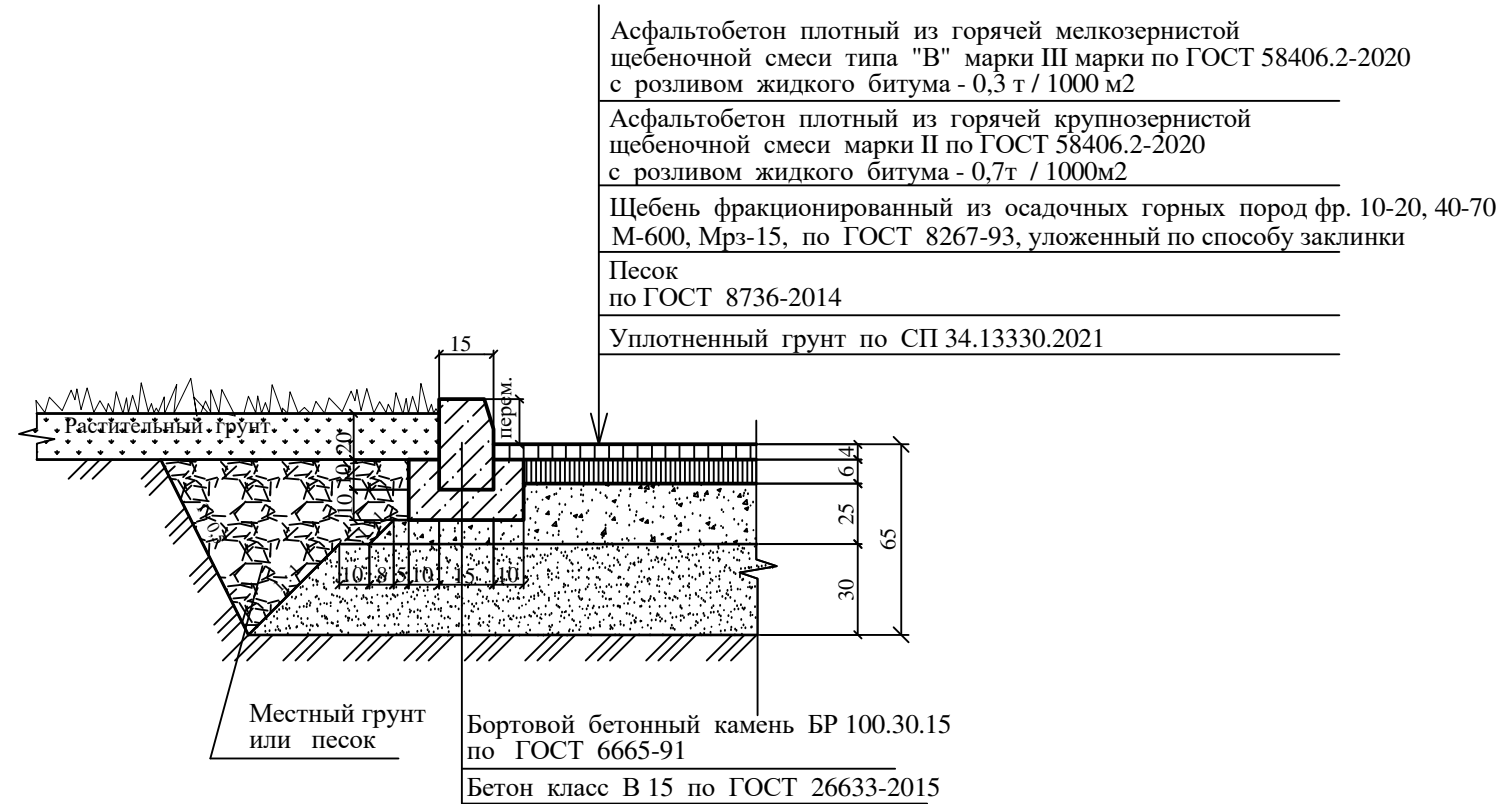


Примечания:

1. Размеры даны в метрах.
2. При продольных уклонах более 30% необходимо устраивать покрытие из мелкозернистого а/б с повышенной шероховатостью (ВСН 36-90).

тип 7 Покрытие буферной зоны вокруг футбольного поля

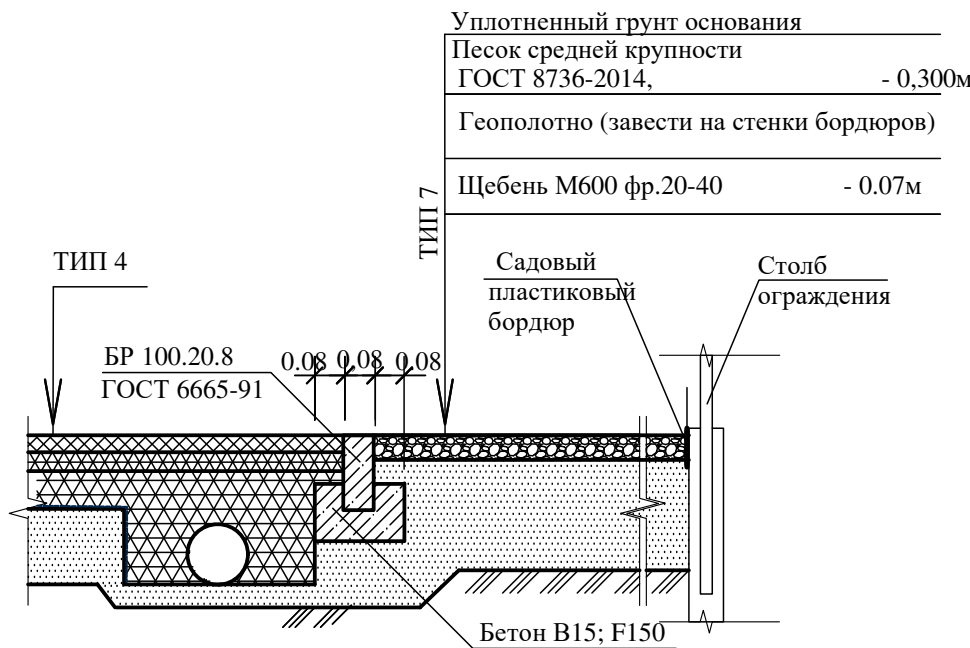

Устройство съезда для инвалидов колясок

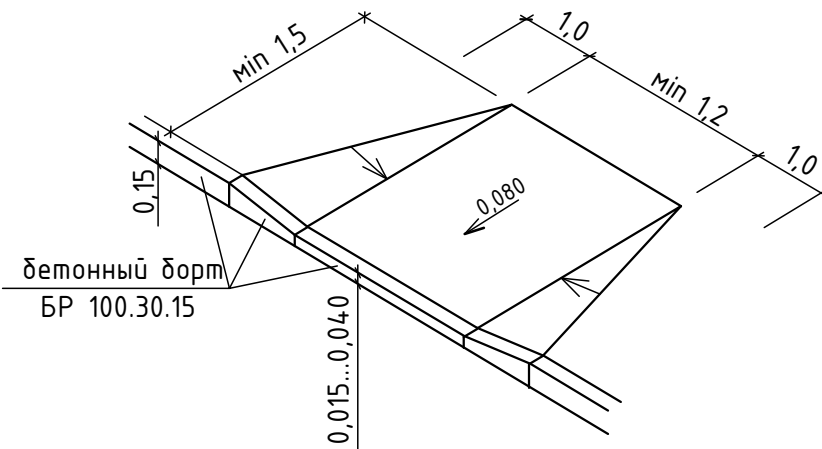

00-ПЗУ					
Устройство модульного спортивного сооружения по адресу: Самарская область, г.о. Самара, Железнодорожный район, ул. Спортивная, на территории земельных участков с кадастровыми номерами 63:01:0104002:1115, 63:01:0104002:1117					
Изм.	Кол.уч	Лист	№ док	Подпись	Дата
Разраб.	Нерода			04.2025	
Схема планировочной организации земельного участка				Стадия	Лист
				п	5
Узлы и детали проездов, тротуарных покрытий и площадок				Общество с ограниченной ответственностью "Самарский Промстройпроект"	
Н.контр.	Шурыгин				
ГИП	Нефедова				

ВЕДОМОСТЬ ОБЪЕМОВ РАБОТ

N п/п	Наименование	Ед. изм.	Количество	Примечание
1.	Ремонт а/б покрытия проезжей части (дет. тип 1)	м ²	415,0	
2.	Покрытие отмотки (дет. тип 2)	м ²	84,0	
3.	Покрытие тротуара (дет. тип 3)	м ²	339,0	
4.	Покрытие футбольного поля (дет. тип 4)	м ²	1147,9	
5.	Покрытие игровой площадки баскетбол (дет. тип 5)	м ²	330,75	
6.	А/б покрытие проезжей части (дет. тип 6)	м ²	530,0	
7.	Установка дорожного борта БР 100х30х15	пм	225,0	
8.	Установка тротуарного борта БР 100х20х8 в том числе для устройства площадок	пм	397,0	
9.	Ограждение спортивных площадок (h=3.0м)	пм	245,0	Ширина панели -2,5м Ячейка панели 50х150мм Кол-во столбов (80мм х 60мм) -110шт.
10.	Ворота / Калитка	шт	1 / 5	
11.	Устройство газонов (посев трав) в том числе: устройство откосов	м ²	1047,5 355,0	Посев многолетних трав с добавлением растительного грунта слоем h=0,2м овсяница луговая 35% овсяница красная 35% клевер красный 30%
12.	Вырубка деревьев с выкарчевкой пней	шт	—	Постановление №119 от 17.04.25 Администрация Железнодорожного района г.о. Самара
13.	Демонтаж сущ. покрытия (асфальт) Демонтаж сущ. площадки (цем-бет)	м ²	3055,0 13,0	
14.	Демонтаж сущ. сооружения (М)	шт	1	
15.	Разборка сущ. борта БР 100х30х15	пм	465,0	
16.	Демонтаж сущ. опор освещения	шт	2	
17.	Демонтаж фундамента опоры ОДН	дхшхг, м	1,0х1,5х5,0	
18.	Покрытие буферной зоны вокруг футбольного поля (дет. тип 7)	м ²	105,0	Устройство системы дренажа см. раздел НВК
19.	Устройство дренажа футбольного поля	пм	147,0	Устройство системы дренажа см. раздел НВК
20.	Георешетка	м ²	355,0	см. лист 2 Примечание 6,7
21.	Площадь земельных участков	м ²	4427,0	
22.	Площадь благоустройства территории	м ²	4463,74	
23.	Установка малых архитектурных форм и оборудования	шт		см. лист 2 Ведомость МАФ

К объемам работ добавить: объемы земляных масс см. лист 4
тренажеры зоны воркаута